ELECTRICAL LEGEND:

SL. NO.	FIXTURES NAME	SYMBOL	FLOORS											TOTAL
			GROUND FLOOR	1ST FLOOR	2ND. FLOOR	3RD. FLOOR	4TH. FLOOR	5TH. FLOOR	6TH. FLOOR	7TH. FLOOR	8TH. FLOOR	9TH. FLOOR	ROOF. FLOOR	
1	CEILING FAN	F	53	61	40	27	39	53	42	42	41	46		444
2	TUBE LIGHT FITTING WITH 4'-40WATT TUBE LAMP	T	36	35	64	45	39	56	50	50	39	35		449
3	CEILING SUSPENDED INDUSTRIAL TYPE TUBE LIGHT FIXTURE. (SUSPENDED WITH DOUBLE BRASS CHAIN OR 12.7MM DIA ANODIZED/CROMIUM PLATED BRASS PIPE OF LENGTH 450 MM) (MODEL HEAVEN'S EPTL-1009X2X40W)	2T	26	36	0	0	9	9	0	0	12	18		110
4	BRACKET LIGHT FITTING WITH 15-WATT ENERGY SAVING LAMP	B	28	29	35	29	21	27	21	21	18	21		250
5	MIRROR LIGHT FITTING WITH 2'-20WATT TUBE LAMP	M	4	4	4	4	4	4	4	4	4	4		40
6	BOX TYPE CEILING LIGHT FITTING WITH 15 WATT ENERGY SAVING LAMP	E	28	22	18	18	20	23	22	22	22	20		215
7	WALL MOUNTED SECURITY (W.T) LIGHT FITTING WITH 20 WATT ENERGY SAVING LAMP	SL	12	0	0	0	0	0	0	0	0	0		12
8	3- PIN 15/16A ROUND & FLAT HOLE SOCKET WITH NEON INDICATOR & SWITCH FOR EQUIPMENTS	QP	30	32	33	24	18	23	8	8	7	6		189
9	3- PIN ROUND HOLE SOCKET WITH 3 TON AC	QPB	0	0	0	0	3	3	0	0	4	4		14
10	3- PIN ROUND HOLE SOCKET WITH 1 TON AC	Q	0	0	13	9	0	0	0	0	0	0		22
11	CONCEALED SWITCH BOARD	SB	26	26	30	23	18	22	18	18	16	18		215
12	2- PIN SOCKET		18	18	20	16	12	15	11	11	10	14		145
13	SUB DISTRIBUTION BOARD (1- PHASE)	SSDB	8	8	0	0	0	4	2	2	0	0		24
14	LIGHITING SUB DISTRIBUTION BOARD (1- PHASE)	LSDB	2	2	2	2	2	2	2	2	2	2		20
15	GENERALPOWER SUB DISTRIBUTION BOARD (1- PHASE)	PSDB	2	2	2	2	1	2	1	1	1	1		15
16	ETHERNET SUB DISTRIBUTION BOARD (1- PHASE)	ESDB	1	1	1	1	1	1	1	1	1	1		10
17	FIRE EXTINGUISHER (A. B. C & E DRY CHEMICAL POWDER TYPE)	FE	1	1	1	1	1	1	1	1	1	1		10
18	FIRE ALARM	FA	2	2	2	2	2	2	2	2	2	2		20
19	HEAT DETACTOR	HD	7	7	7	7	7	7	7	7	7	7		10
20	HOSE BOX	HB	1	1	1	1	1	1	1	1	1	1		10
21	INTERNET CONNECTION PORT		0	0	0	0	3	17	2	2	0	1		25
22	CYLINDRICAL TYPE CEILING LIGHT FITTING WITH 15 WATT ENERGY SAVING LAMP	CE	4	4	12	4	4	4	4	4	4	4		48
23	3PIN SOCKET + 2PIN SOCKET+ ETHERNET PORT BOX	QPB	0	0	0	0	0	14	0	0	0	0		14
24	LIGHTING ARRESTOR TEST POINT BOX	LIGHTNING ARRESTOR	2	0	0	0	0	0	0	0	0	0		2
25	EARTHINGFOR LIGHTING PROTECTION	ER	2	0	0	0	0	0	0	0	0	0		2

ELECTRICAL FIXTURES DATA WITH SYMBOL AND QUANTITY

DESIGN DATA

MOUNTING HEIGHT OF ELECTRICAL FITTINGS

LIST OF ITEM	HEIGHT FROM FFL	REMARKS
01. SWITCH	1350 mm	**AS PER SITE REQUIREMENT WITH CONSENT OF RELEVANT DESIGN ENGINEER**
02. DP SWITCH	1350 mm	
03. FAN REGULATOR	1350 mm	
04. 05A SOCKET OUTLET	300 mm/1350 mm	
05. 15/16 A SOCKET OUTLET	300 mm	
06. AC SPLIT SOCKET POINT	2250 mm	
07. GEYSER SOCKET POINT	2100 mm	
08. DP SWITCH/SOCKET POINT FOR AC, GEYSER	1350 mm 1500 mm	
09. DISTRIBUTION BOARD	300 mm	
10. TELEPHONE, LAN, INTERCOM	1200 mm	
11. DISH ANTENNA OUTLET		


SCHEDULE OF SINGLE CORE CABLES IN CONDUITS AS PER BNBC

COPPER CONDUCTOR SIZE IN mm^2 (TYPE-BYA/BYM)	CONDUIT INNER DIAMETER (mm)				
	20 mm	25 mm	32 mm	38 mm	50 mm
	MAXIMUM NUMBER OF CABLES				
1.5	06	10	14	--	--
2.5	05	10	14	--	--
4.0	03	06	10	14	--
6.0	02	05	08	11	--
10	--	04	07	09	--
16	--	02	04	05	12
25	--	--	02	02	06

GENERAL NOTES FOR ELECTRICAL FITTINGS


A. UNLESS OTHERWISE SPECIFIED. THE CONDUIT SIZE SHALL BE 20 mm (3/4") INNER DIA
B. WIRING FROM SWITCH BOARD TO LIGHT/FAN POINT WILL BE 2X1C-1.5mm^2 BYM CABLE.
C. OTHERS WIRING SHALL BE AS PER CIRCUIT DIAGRAM.
D. A DP SWITCH MUST CONSIDER WITH SPLIT AC CIRCUIT.
E. THE POINTS IN THE POWER BOX WILL REMAIN 6mm BELOW IT'S COVER LEVEL TO ENSURE SAFETY

EDUCATION ENGINEERING DEPARTMENT MINISTRY OF EDUCATION SHIKKHA BHABAN, DHAKA	**NAME OF PROJECT:** **ESTABLISMENTS OF (04) FOUR NOS ENGINEERING COLLEGE AT CHATTOGRAM,KHULNA,RAJSHAHI & RNGPUR DIVISION**	**NAME OF WORKS:** **CONSTRUCTION OF 10(TEN) STORIED ACADEMIC BUILDING (CIVIL ENGINEERING) WITH 10 STORIED FOUNDATION**	**SHEET NO:- 1** **DWG. NO: 04** **Date: 19/01/26**	**JUBAYER AZAD JIM** DRAFTSMAN	**Md. Hedayatul Islam** ASSISTANT ENGINEER	**Atikur Rahman Talukder** EXECUTIVE ENGINEER	**PROTIVA SARKAR** SUPERINTENDING ENGINEER	**Md. Tareque Anwar Zahedee** CHIEF ENGINEER

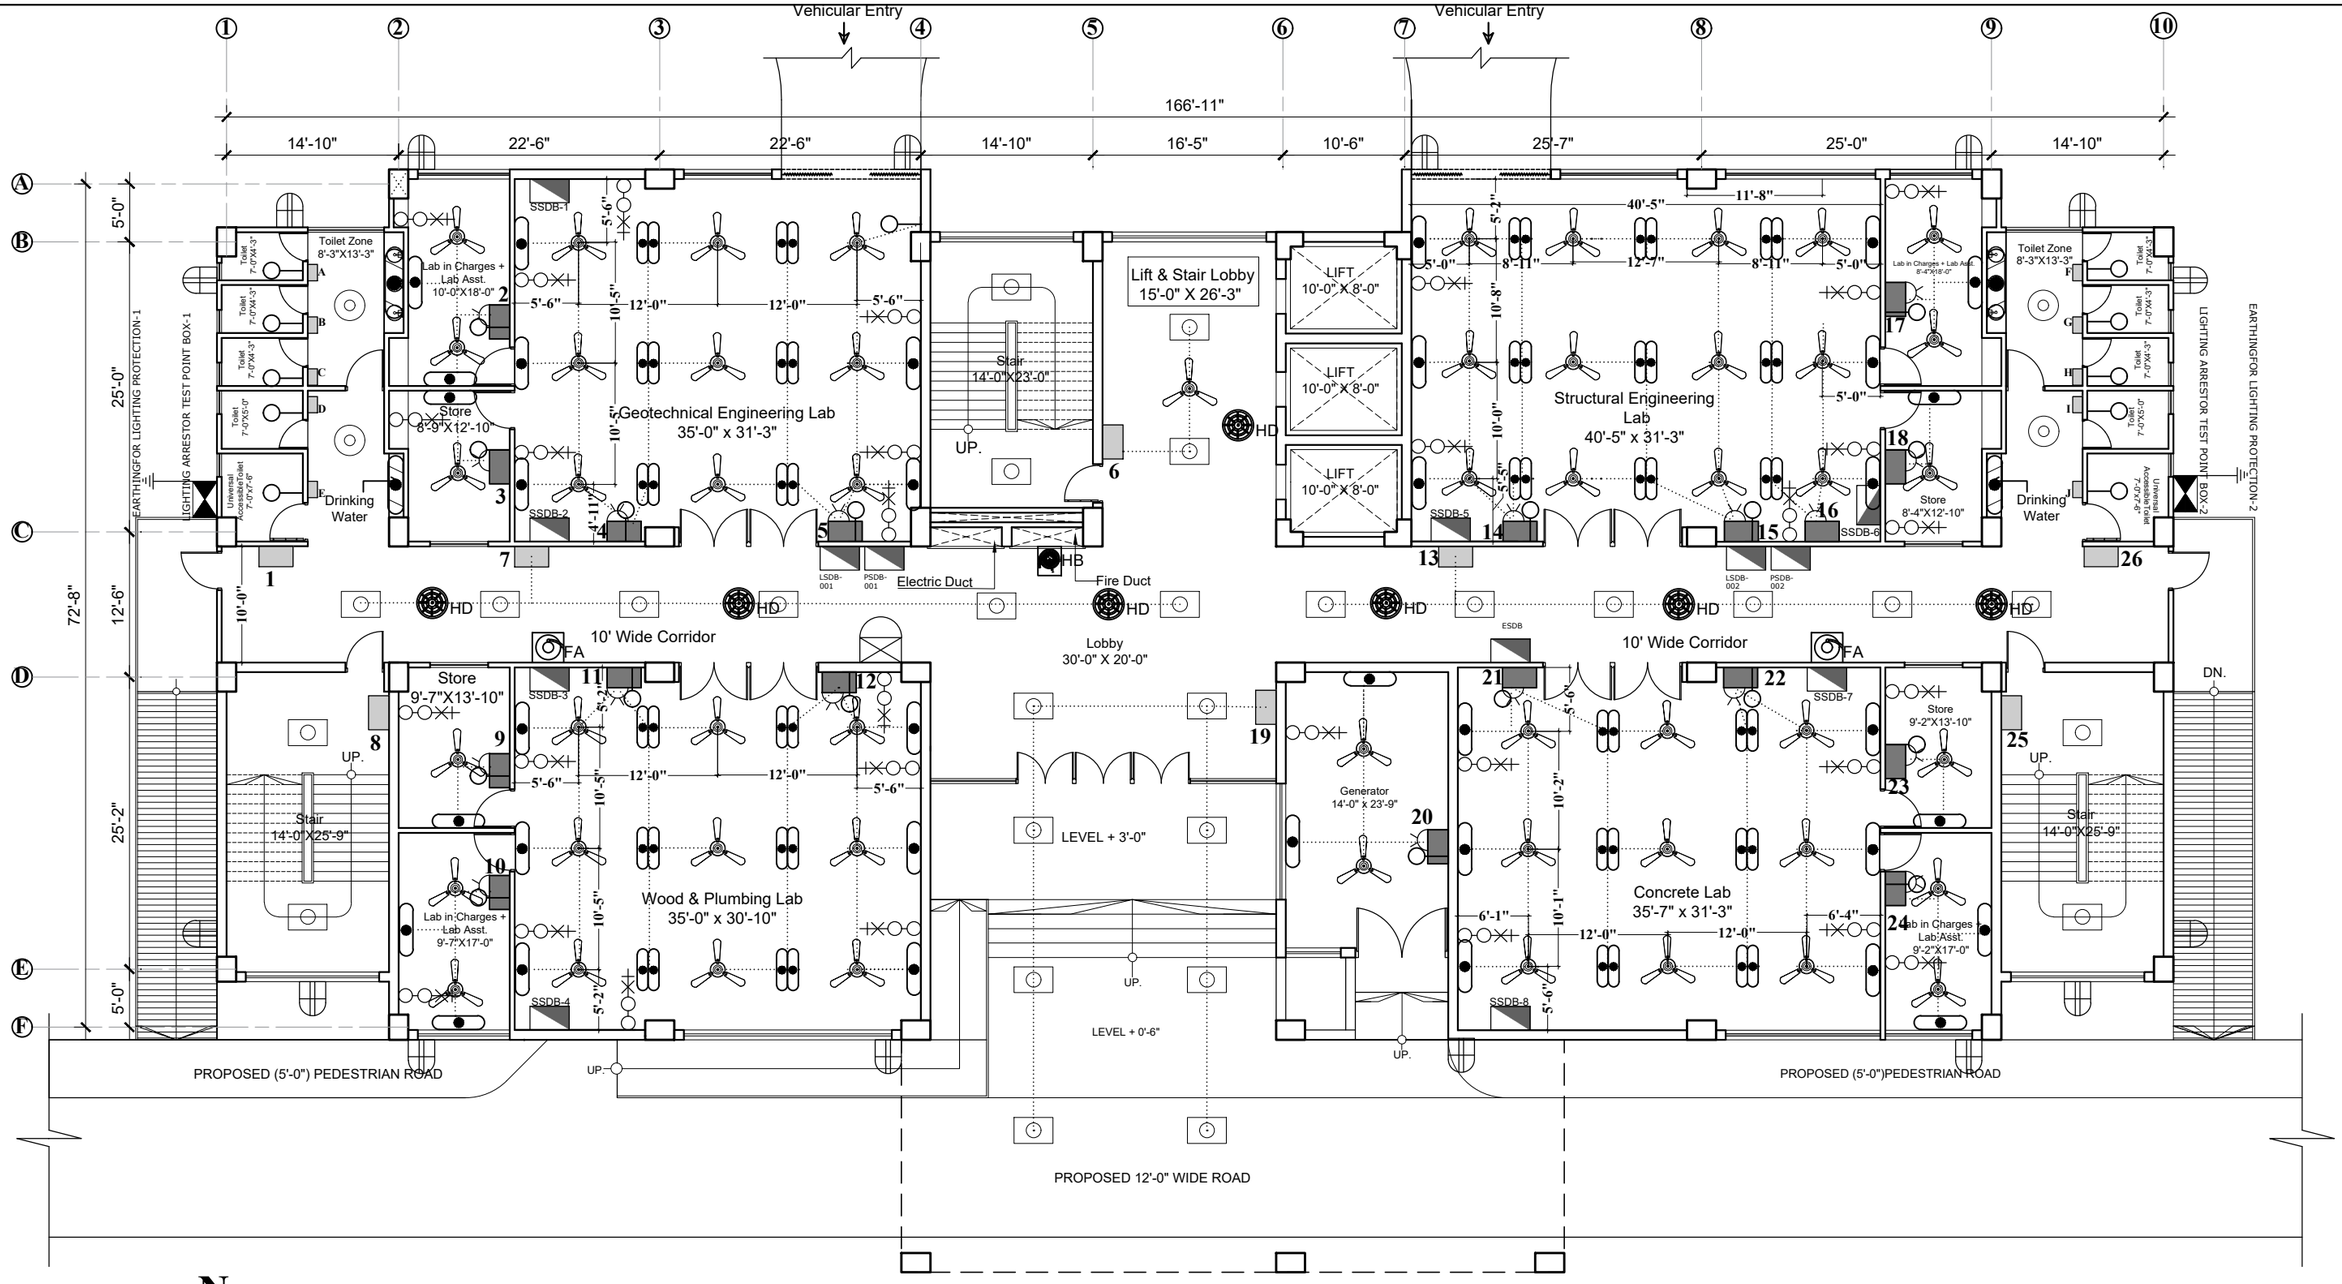


ELECTRICAL FIXTURE LAYOUT PLAN
GF FLOOR PLAN

EDUCATION ENGINEERING DEPARTMENT MINISTRY OF EDUCATION SHIKKHA BHABAN, DHAKA	NAME OF PROJECT: ESTABLISMENTS OF (04) FOUR NOS ENGINEERING COLLEGE AT CHATTOGRAM,KHULNA,RAJSHAHI & RNGPUR DIVISION	NAME OF WORKS: CONSTRUCTION OF 10(TEN) STORIED ACADEMIC BUILDING (CIVIL ENGINEERING) WITH 10 STORIED FOUNDATION	SHEET NO:- 2 DWG. NO: 04 Date: 19/01/26	JUBAYER AZAD JIM DRAFTSMAN	Md. Hedayatul Islam ASSISTANT ENGINEER	Atikur Rahman Talukder EXECUTIVE ENGINEER	PROTIVA SARKAR SUPERINTENDING ENGINEER	Md. Tareque Anwar Zahedee CHIEF ENGINEER

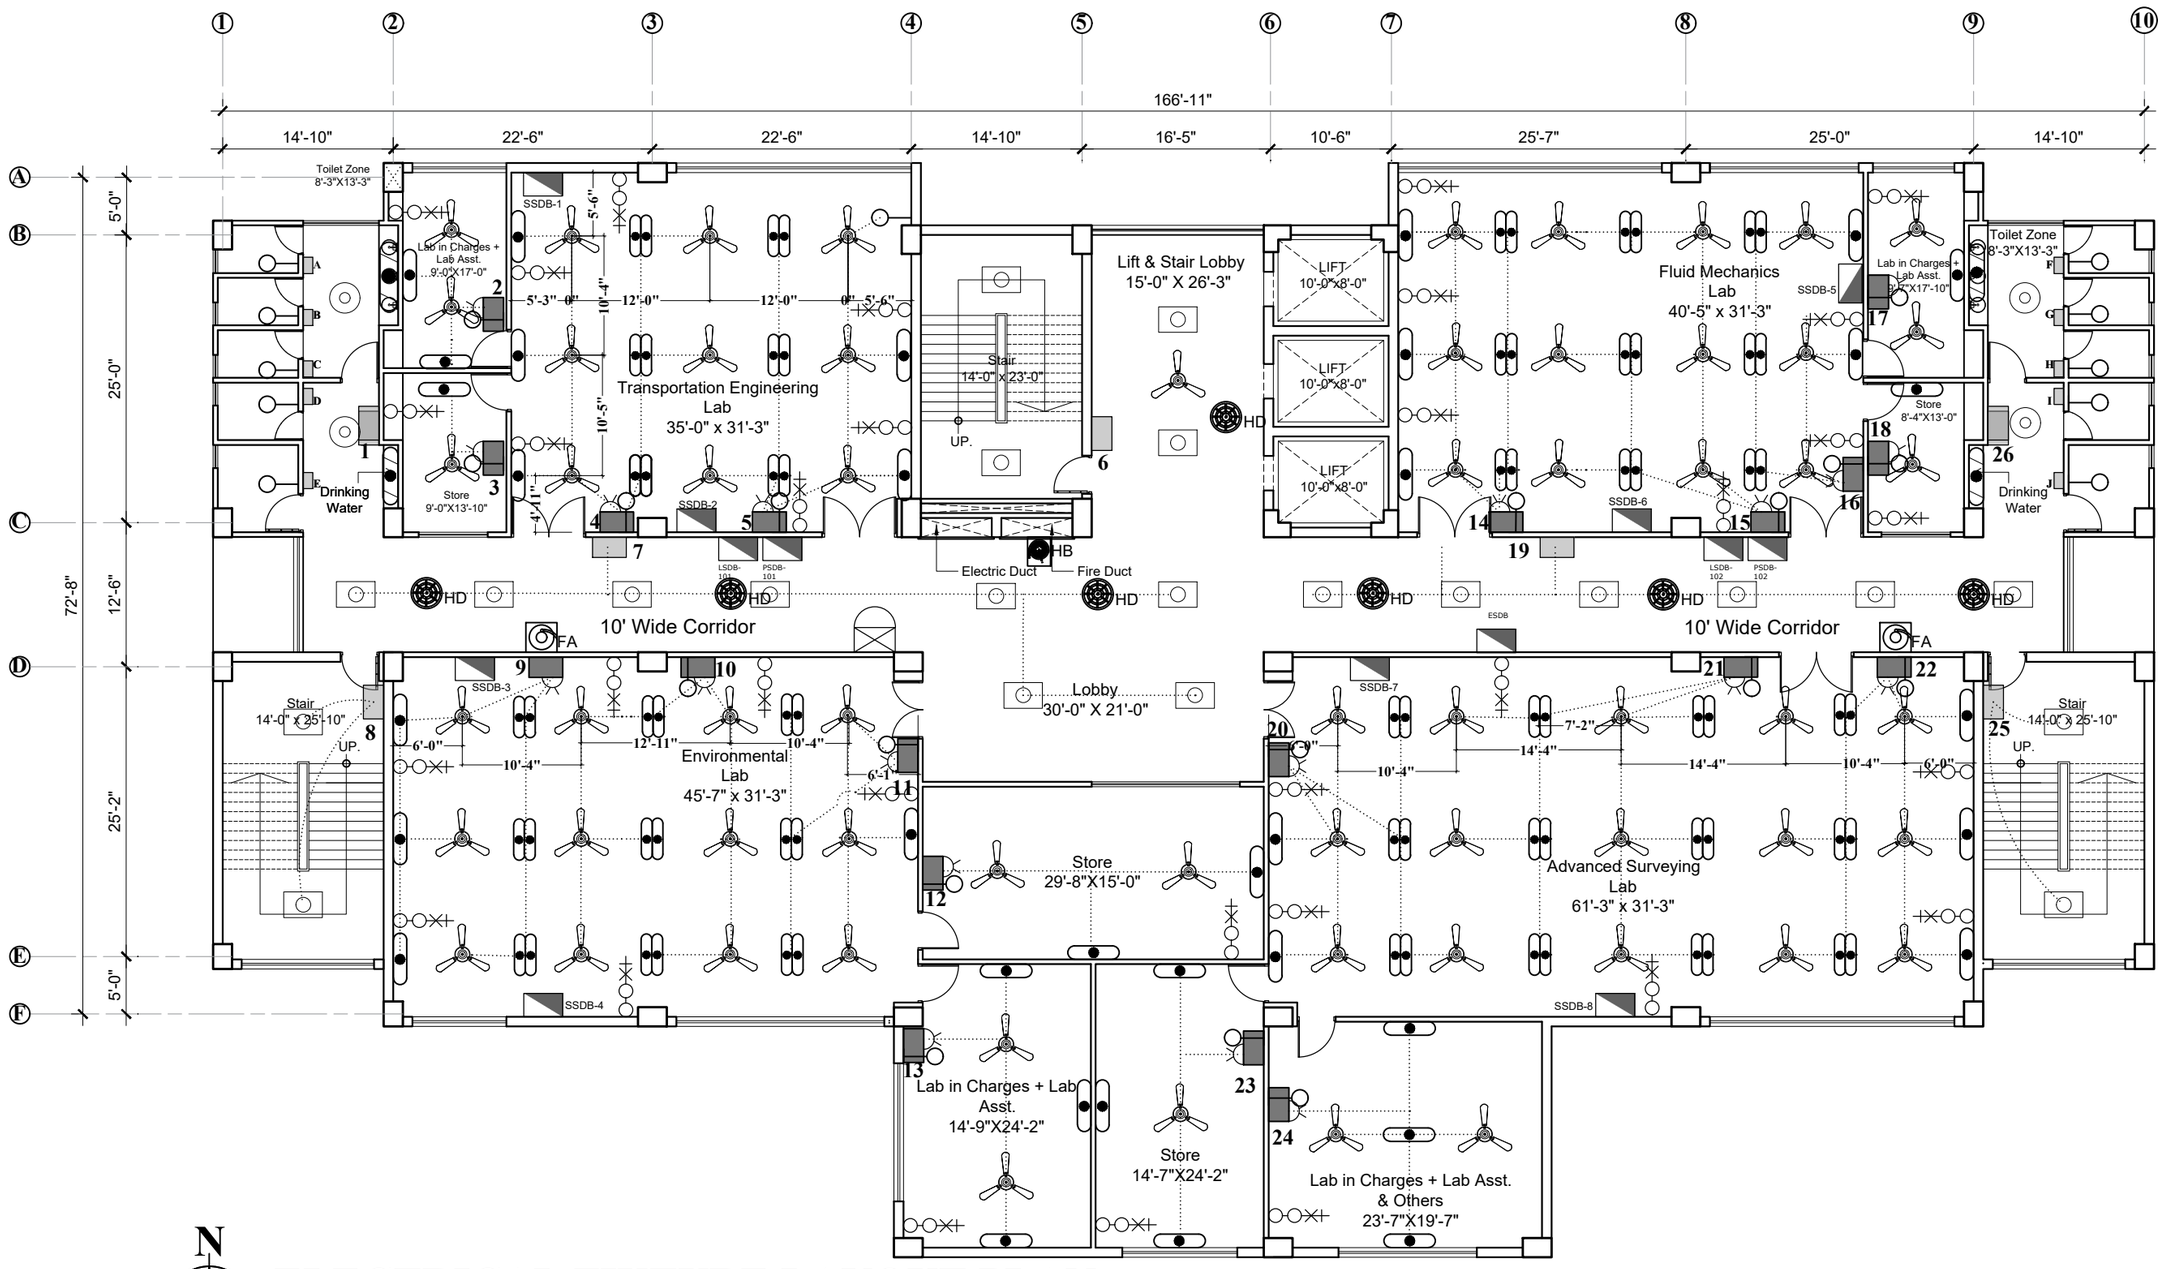

ELECTRICAL FIXTURE LAYOUT PLAN
1ST FLOOR PLAN


EDUCATION ENGINEERING DEPARTMENT MINISTRY OF EDUCATION SHIKKHA BHABAN, DHAKA	NAME OF PROJECT: ESTABLISMENTS OF (04) FOUR NOS ENGINEERING COLLEGE AT CHATTOGRAM,KHULNA,RAJSHAHI & RNGPUR DIVISION	NAME OF WORKS: CONSTRUCTION OF 10(TEN) STORIED ACADEMIC BUILDING (CIVIL ENGINEERING) WITH 10 STORIED FOUNDATION	SHEET NO:- 3 DWG. NO: 04 Date: 19/01/26	JUBAYER AZAD JIM DRAFTSMAN	Md. Hedayatul Islam ASSISTANT ENGINEER	Atikur Rahman Talukder EXECUTIVE ENGINEER	PROTIVA SARKAR SUPERINTENDING ENGINEER	Md. Tareque Anwar Zahedee CHIEF ENGINEER

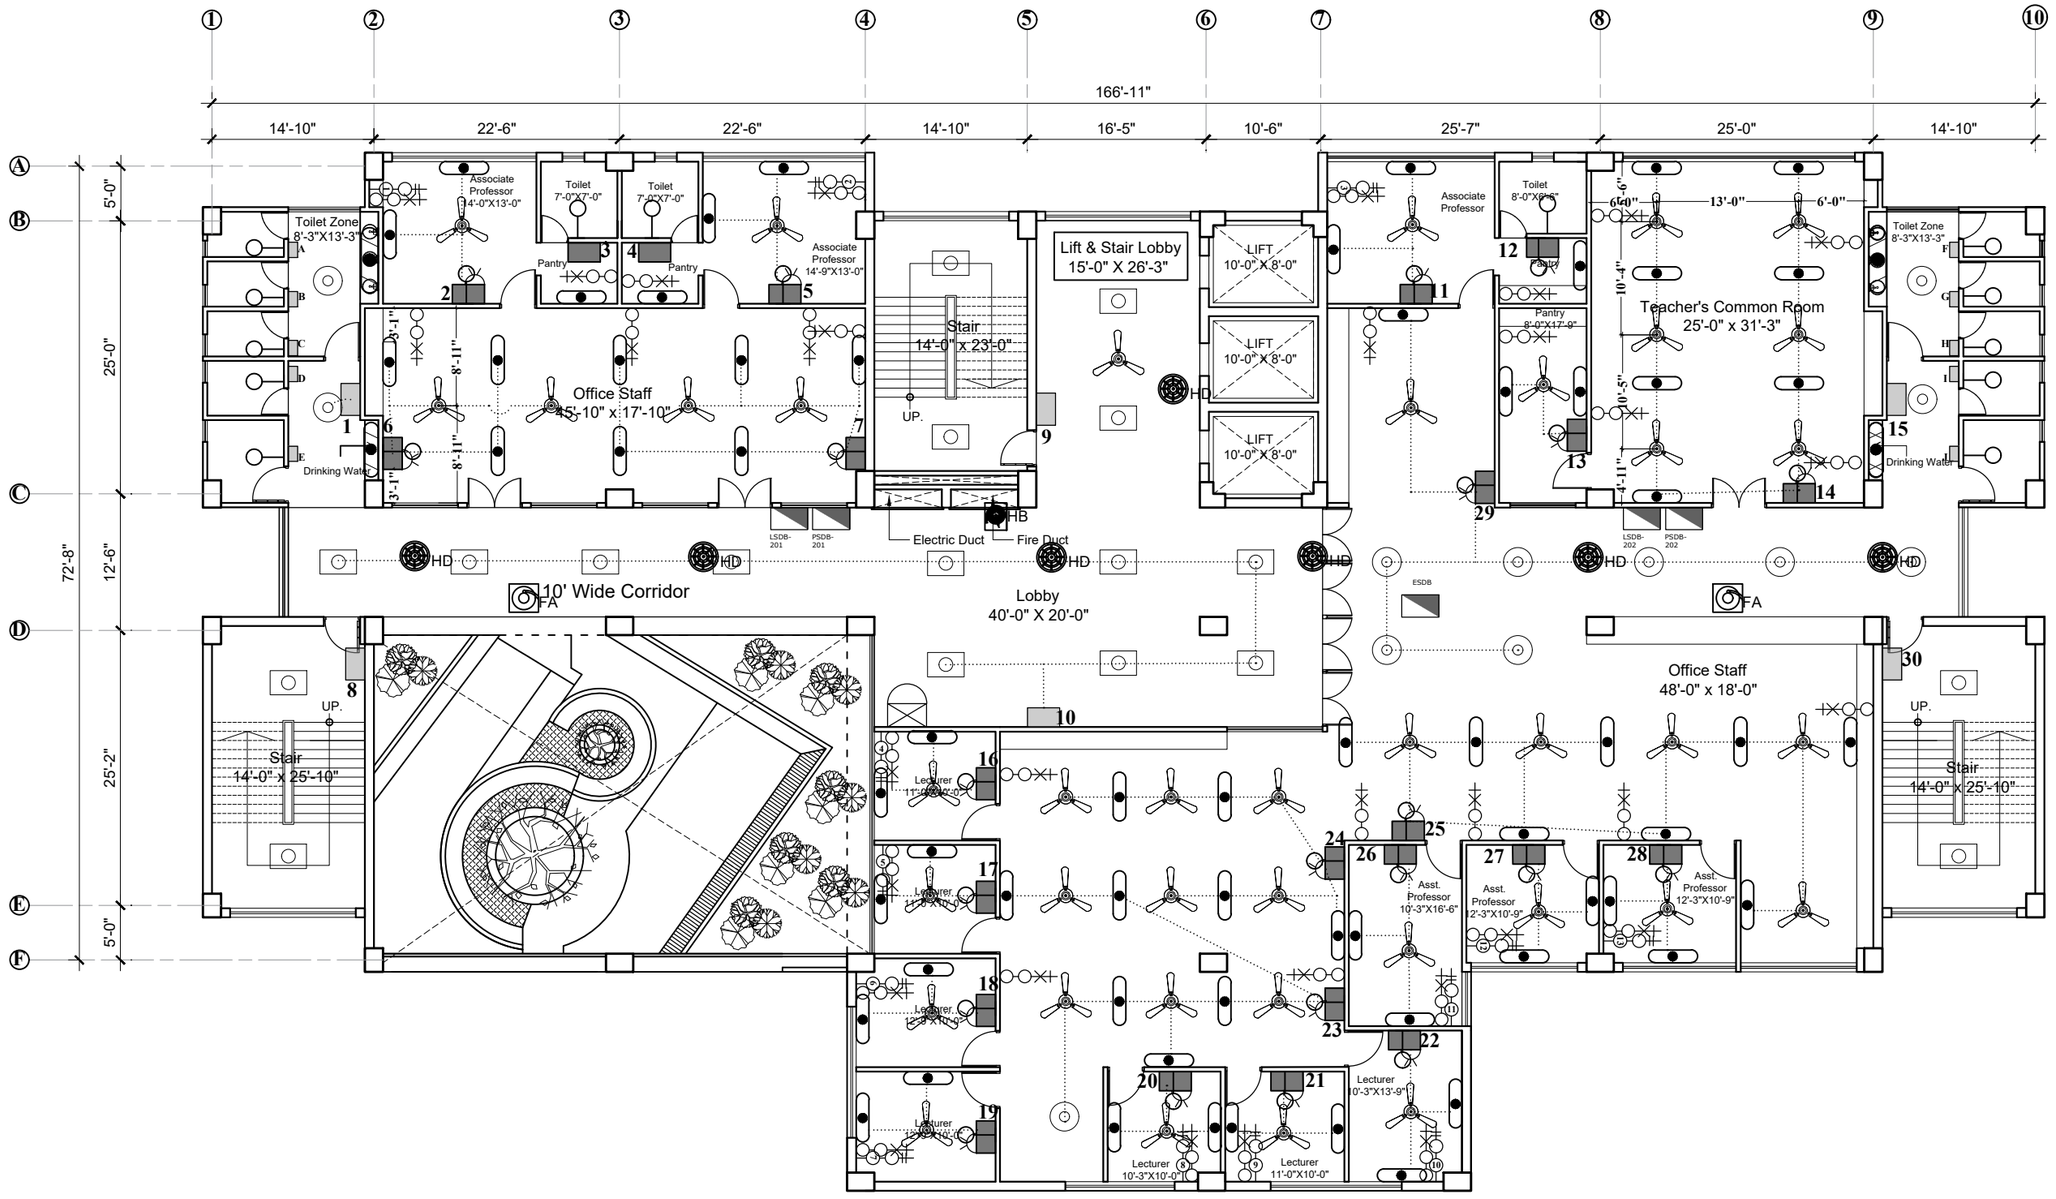

N

ELECTRICAL FIXTURE LAYOUT PLAN
2ND FLOOR PLAN


EDUCATION ENGINEERING DEPARTMENT MINISTRY OF EDUCATION SHIKKHA BHABAN, DHAKA	NAME OF PROJECT: ESTABLISMENTS OF (04) FOUR NOS ENGINEERING COLLEGE AT CHATTOGRAM,KHULNA,RAJSHAHI & RNGPUR DIVISION	NAME OF WORKS: CONSTRUCTION OF 10(TEN) STORIED ACADEMIC BUILDING (CIVIL ENGINEERING) WITH 10 STORIED FOUNDATION	SHEET NO:- 4 DWG. NO: 04 Date: 19/01/26	JUBAYER AZAD JIM DRAFTSMAN	Md. Hedayatul Islam ASSISTANT ENGINEER	Atikur Rahman Talukder EXECUTIVE ENGINEER	PROTIVA SARKAR SUPERINTENDING ENGINEER	Md. Tareque Anwar Zahedee CHIEF ENGINEER

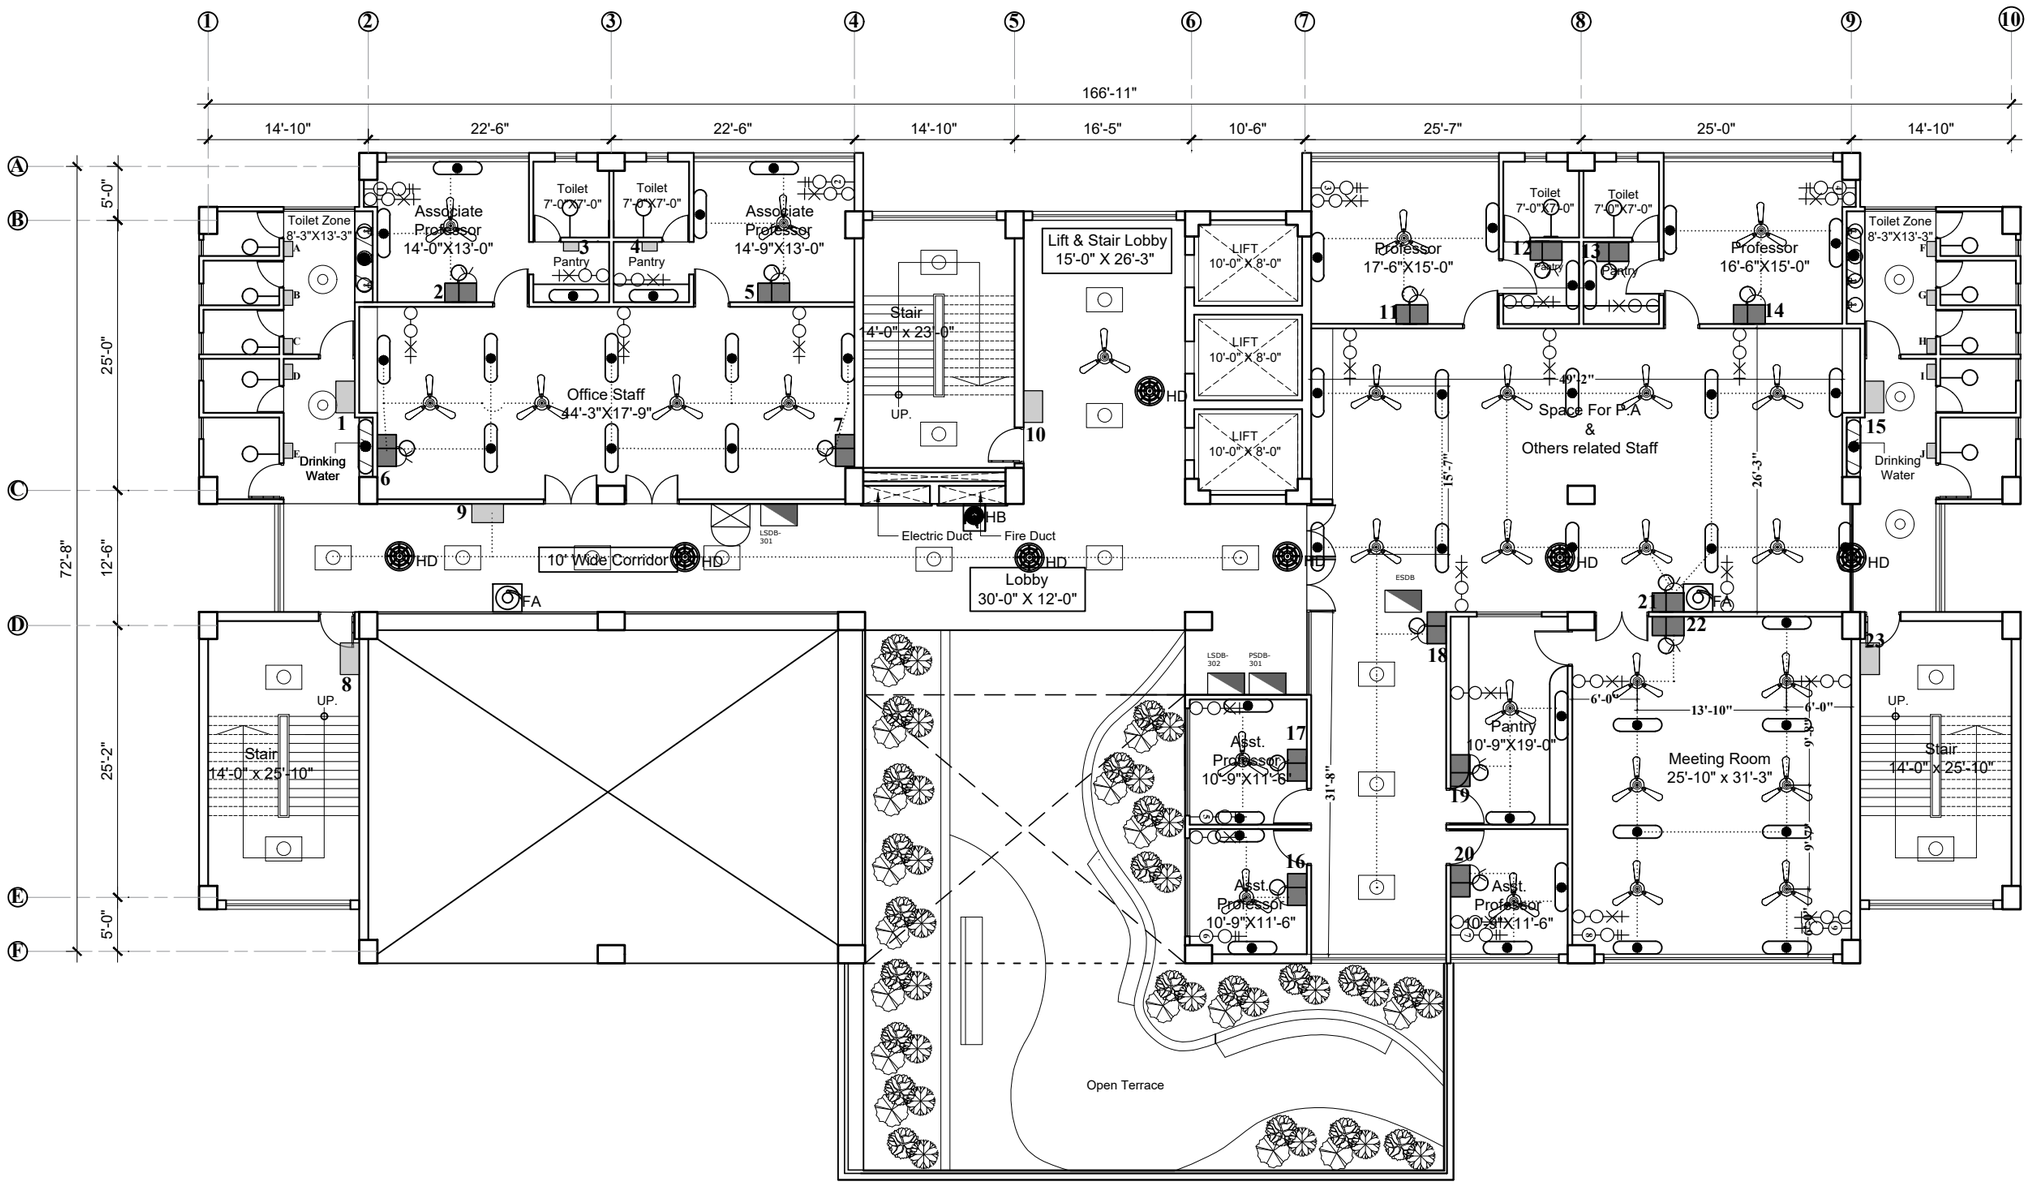

N

ELECTRICAL FIXTURE LAYOUT PLAN
3RD FLOOR PLAN


EDUCATION ENGINEERING DEPARTMENT MINISTRY OF EDUCATION SHIKKHA BHABAN, DHAKA	NAME OF PROJECT: ESTABLISMENTS OF (04) FOUR NOS ENGINEERING COLLEGE AT CHATTOGRAM,KHULNA,RAJSHAHI & RNGPUR DIVISION	NAME OF WORKS: CONSTRUCTION OF 10(TEN) STORIED ACADEMIC BUILDING (CIVIL ENGINEERING) WITH 10 STORIED FOUNDATION	SHEET NO:- 5 DWG. NO: 04 Date: 19/01/26	JUBAYER AZAD JIM DRAFTSMAN	Md. Hedayatul Islam ASSISTANT ENGINEER	Atikur Rahman Talukder EXECUTIVE ENGINEER	PROTIVA SARKAR SUPERINTENDING ENGINEER	Md. Tareque Anwar Zahedee CHIEF ENGINEER

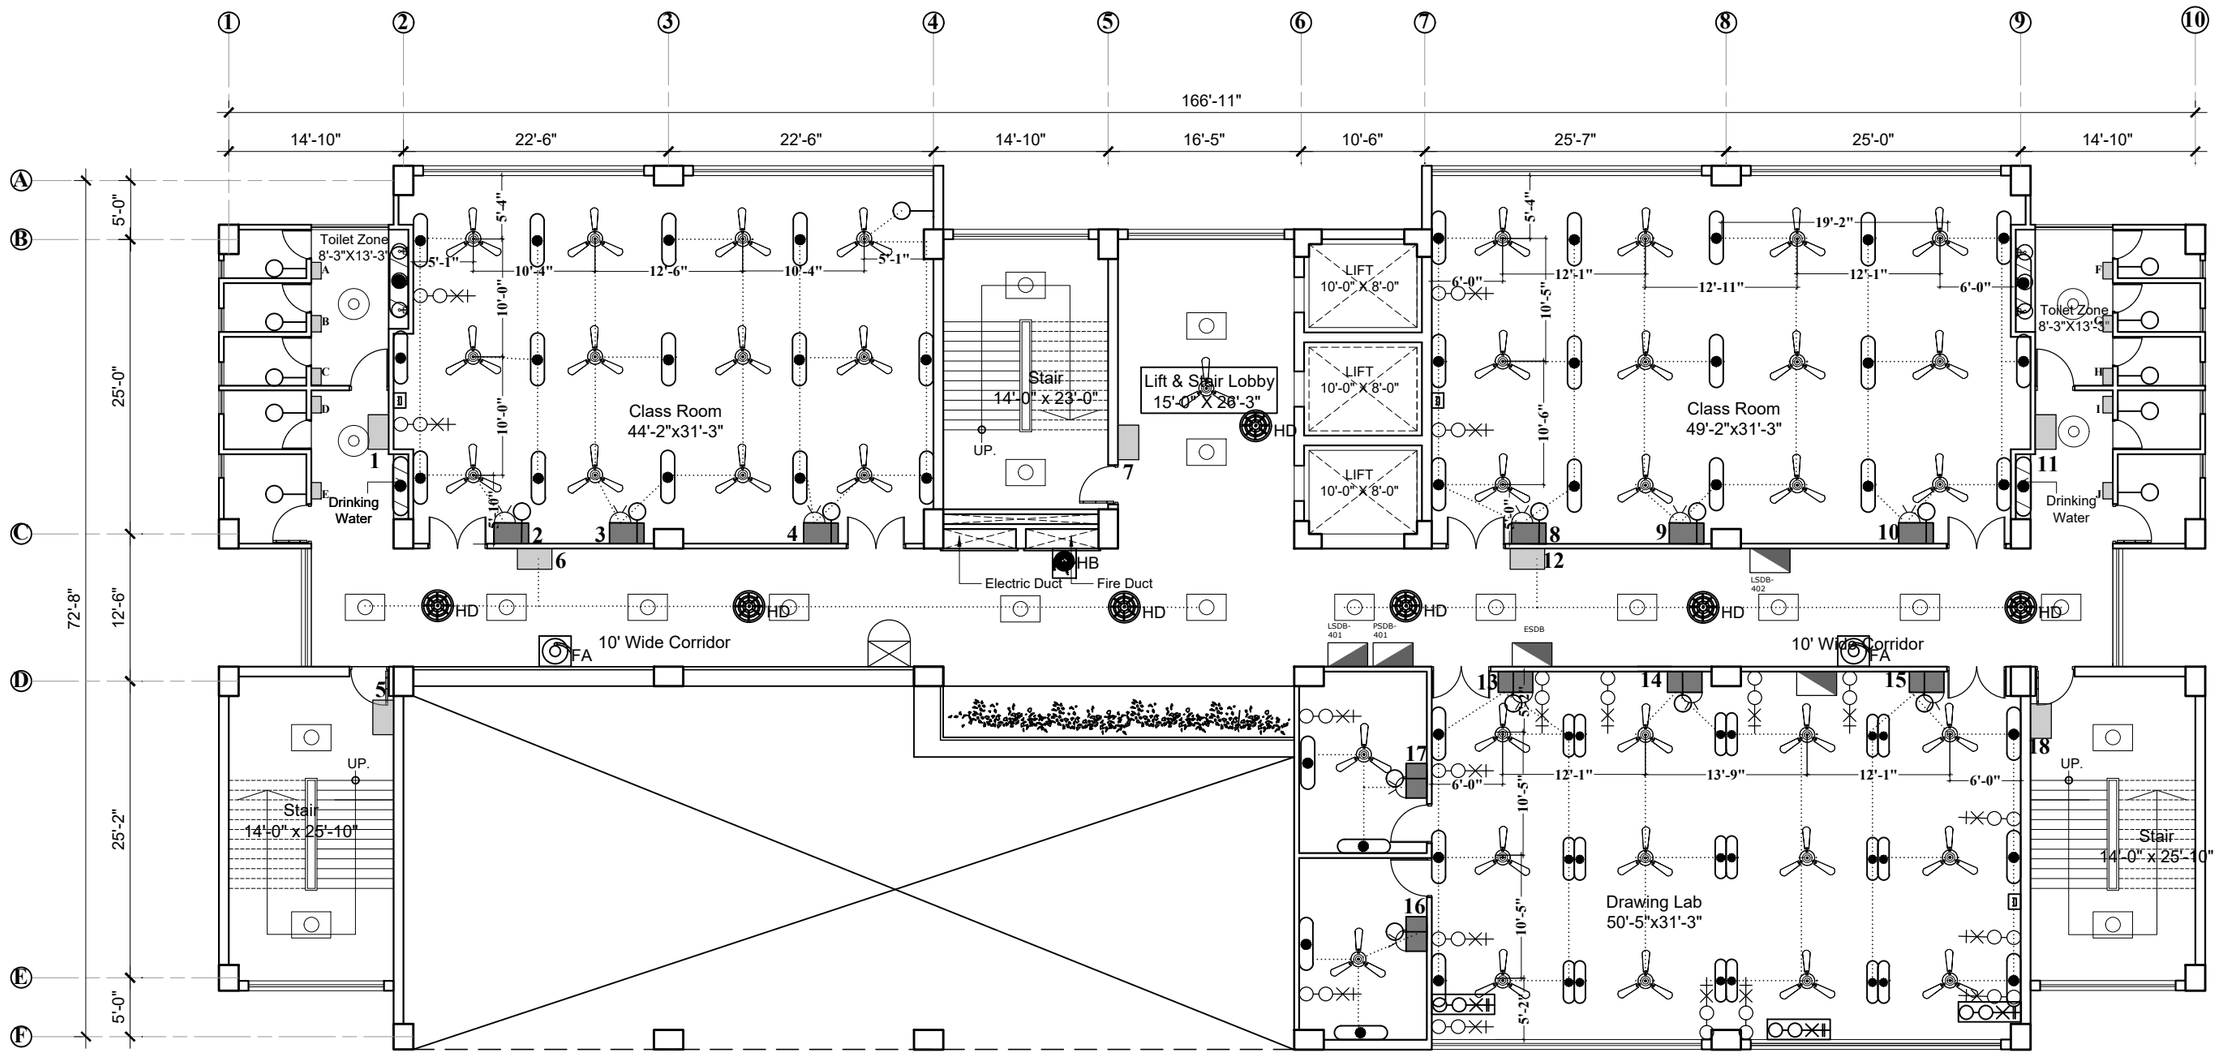

N

ELECTRICAL FIXTURE LAYOUT PLAN
4TH FLOOR PLAN


EDUCATION ENGINEERING DEPARTMENT MINISTRY OF EDUCATION SHIKKHA BHABAN, DHAKA	NAME OF PROJECT: ESTABLISMENTS OF (04) FOUR NOS ENGINEERING COLLEGE AT CHATTOGRAM,KHULNA,RAJSHAHI & RNGPUR DIVISION	NAME OF WORKS: CONSTRUCTION OF 10(TEN) STORIED ACADEMIC BUILDING (CIVIL ENGINEERING) WITH 10 STORIED FOUNDATION	SHEET NO:- 6 DWG. NO: 04 Date: 19/01/26	JUBAYER AZAD JIM DRAFTSMAN	Md. Hedayatul Islam ASSISTANT ENGINEER	Atikur Rahman Talukder EXECUTIVE ENGINEER	PROTIVA SARKAR SUPERINTENDING ENGINEER	Md. Tareque Anwar Zahedee CHIEF ENGINEER

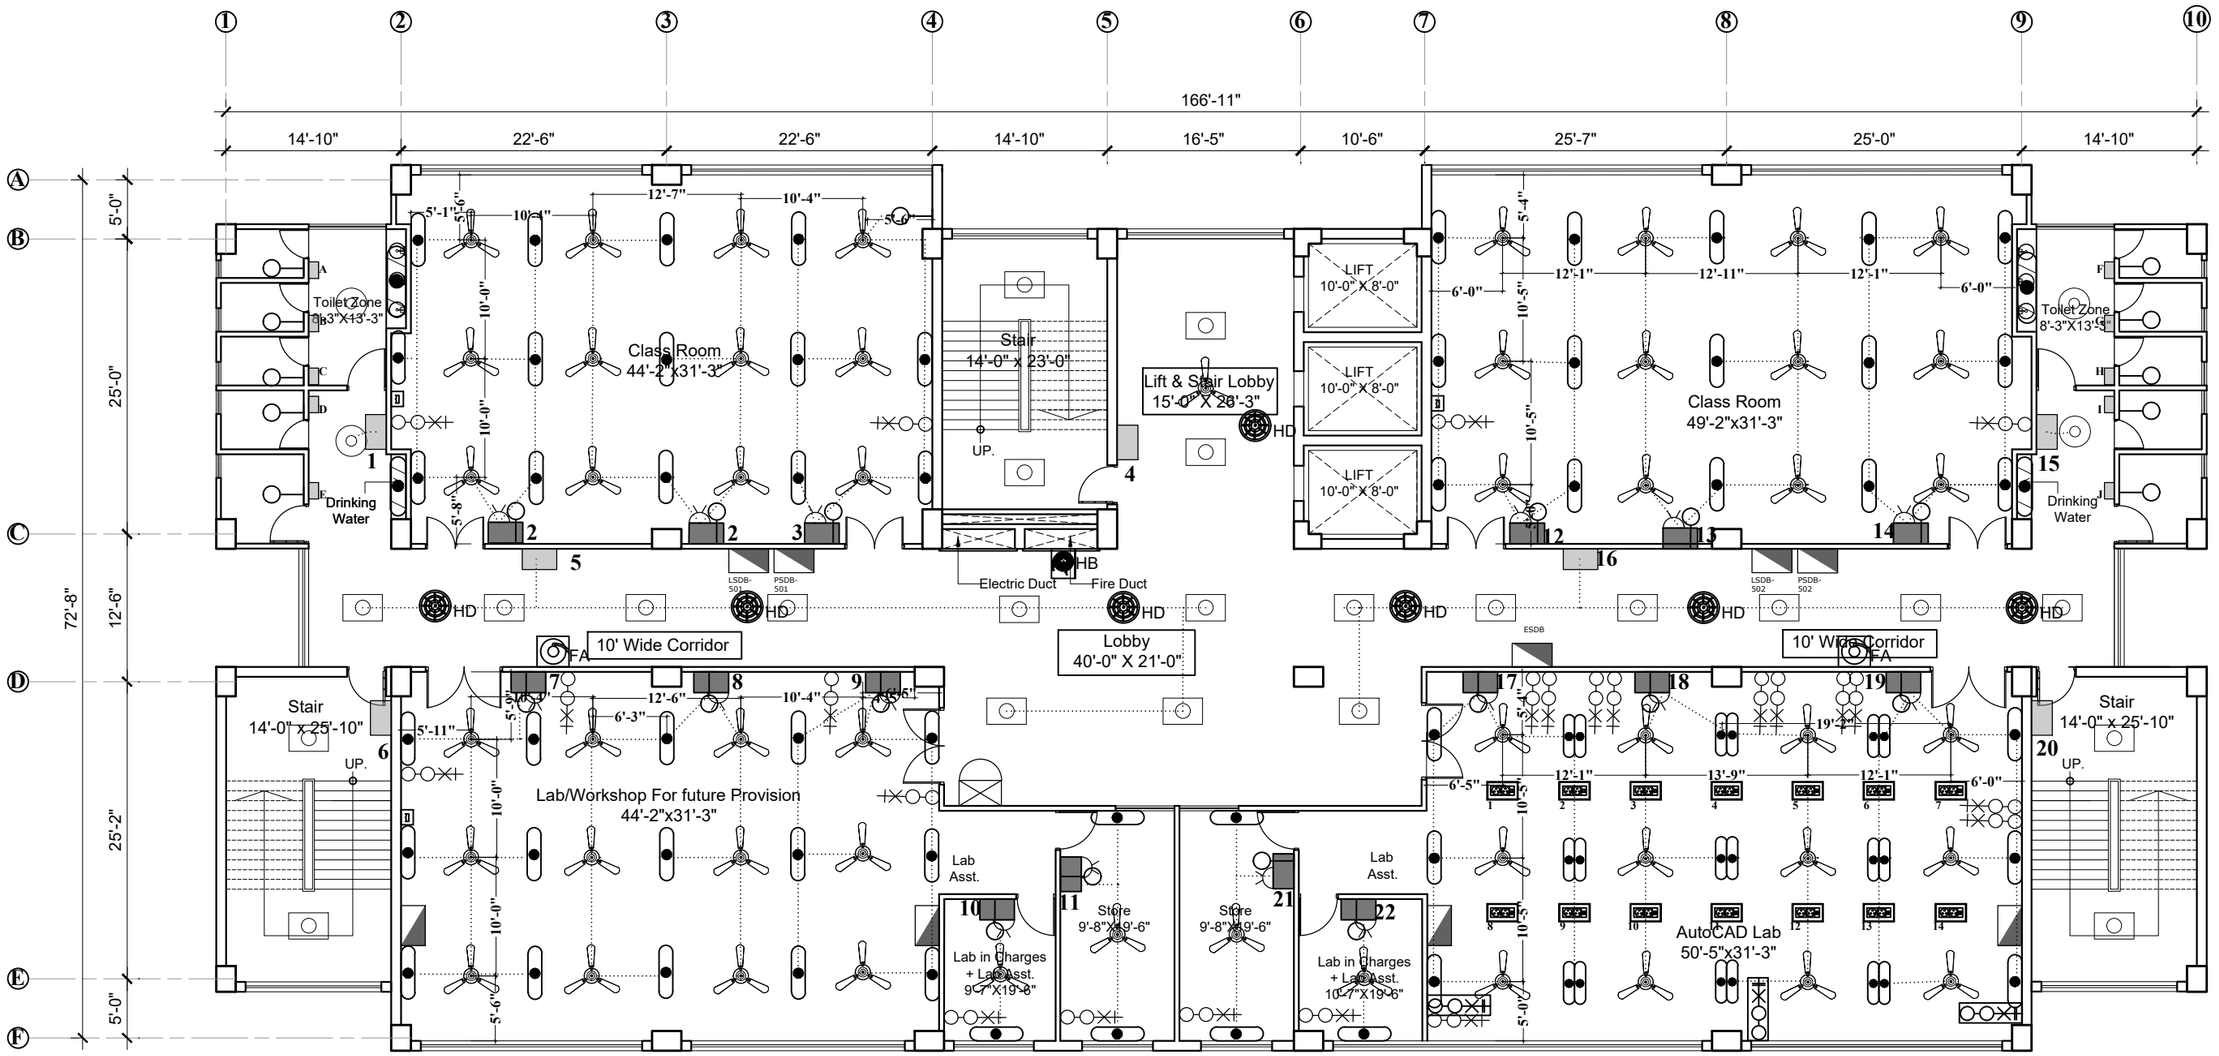

N


ELECTRICAL FIXTURE LAYOUT PLAN
5TH FLOOR PLAN

EDUCATION ENGINEERING DEPARTMENT MINISTRY OF EDUCATION SHIKKHA BHABAN, DHAKA	NAME OF PROJECT: ESTABLISMENTS OF (04) FOUR NOS ENGINEERING COLLEGE AT CHATTOGRAM,KHULNA,RAJSHAHI & RNGPUR DIVISION	NAME OF WORKS: CONSTRUCTION OF 10(TEN) STORIED ACADEMIC BUILDING (CIVIL ENGINEERING) WITH 10 STORIED FOUNDATION	SHEET NO:- 7 DWG. NO: 04 Date: 19/01/26	JUBAYER AZAD JIM DRAFTSMAN	Md. Hedayatul Islam ASSISTANT ENGINEER	Atikur Rahman Talukder EXECUTIVE ENGINEER	PROTIVA SARKAR SUPERINTENDING ENGINEER	Md. Tareque Anwar Zahedee CHIEF ENGINEER

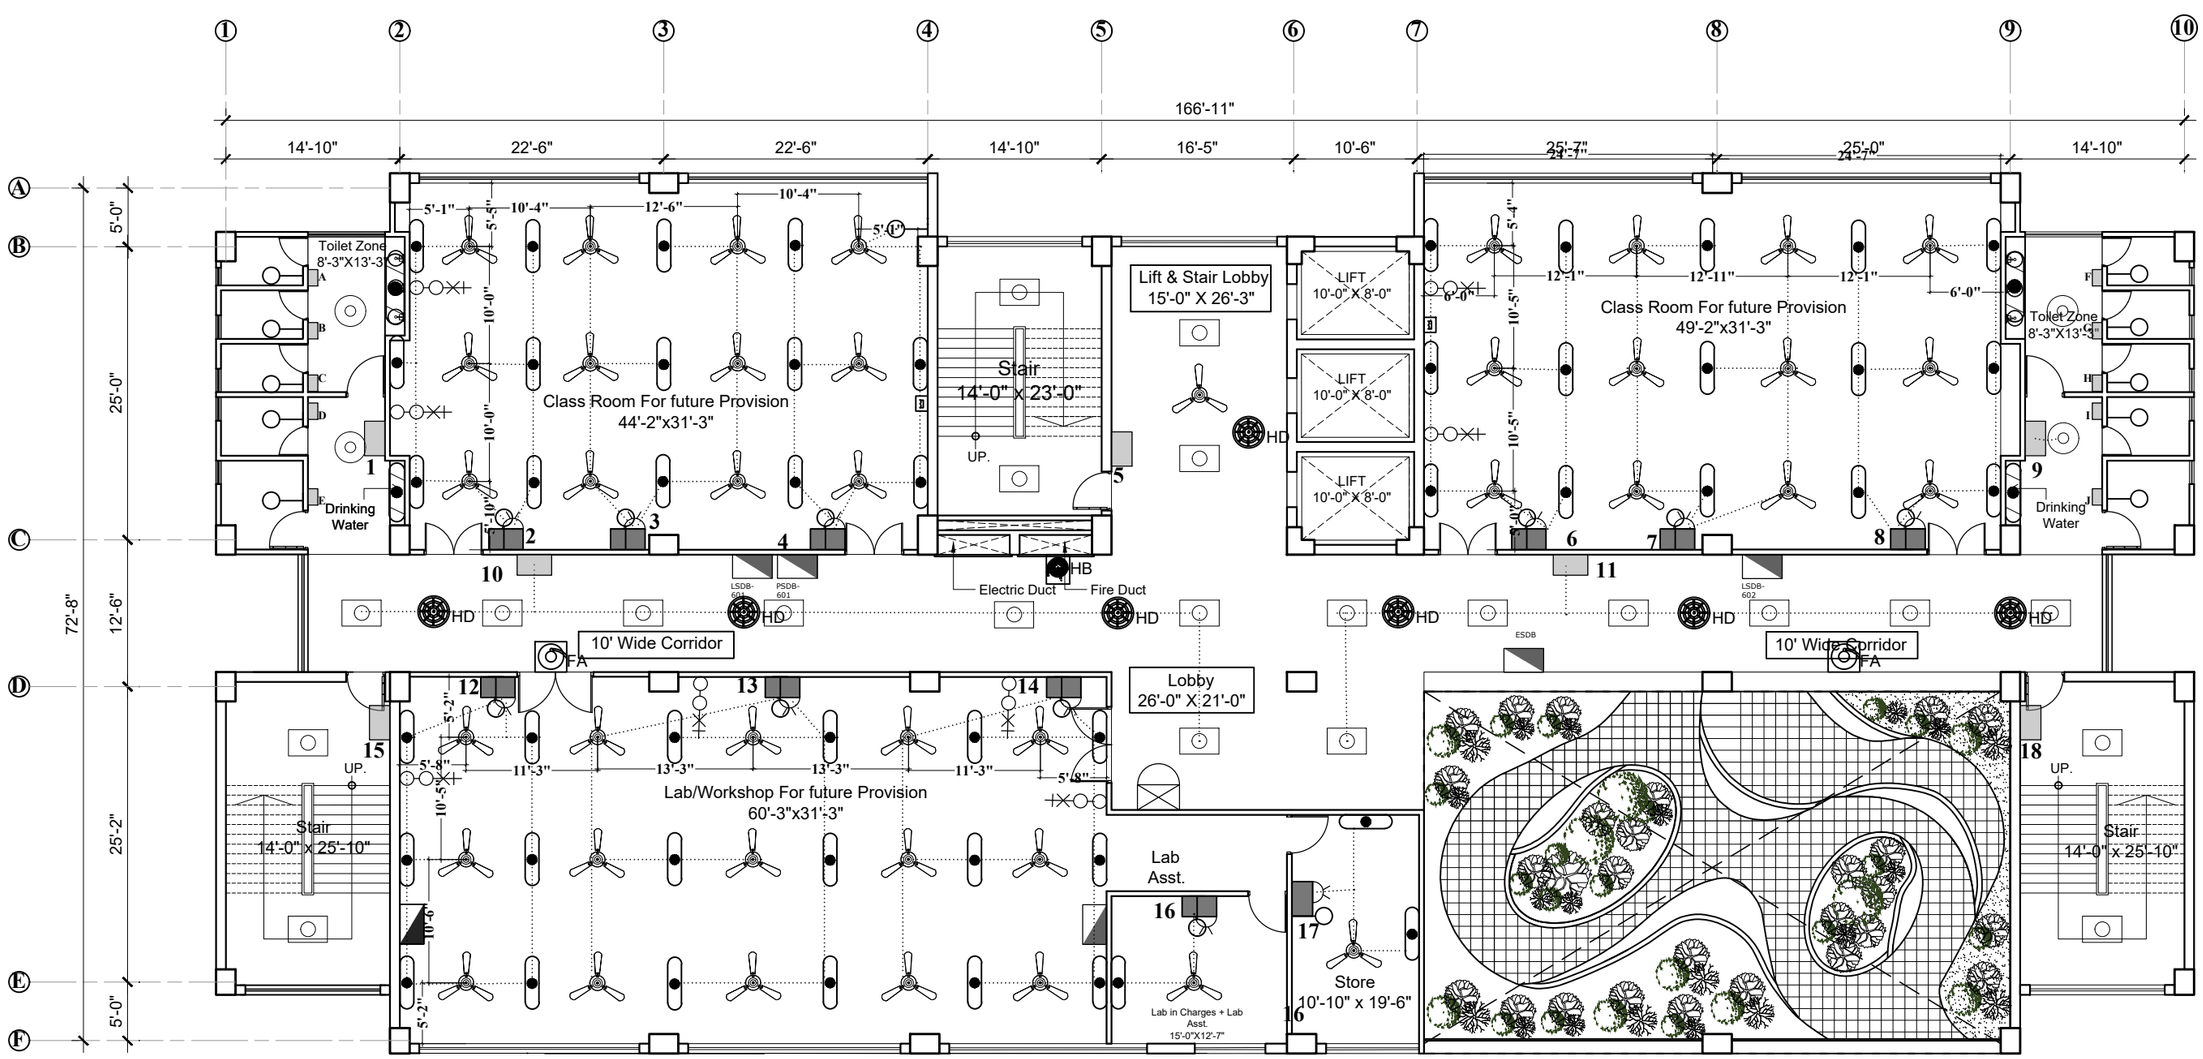


ELECTRICAL FIXTURE LAYOUT PLAN
6TH FLOOR PLAN

EDUCATION ENGINEERING DEPARTMENT MINISTRY OF EDUCATION SHIKKHA BHABAN, DHAKA	NAME OF PROJECT: ESTABLISMENTS OF (04) FOUR NOS ENGINEERING COLLEGE AT CHATTOGRAM,KHULNA,RAJSHAHI & RNGPUR DIVISION	NAME OF WORKS: CONSTRUCTION OF 10(TEN) STORIED ACADEMIC BUILDING (CIVIL ENGINEERING) WITH 10 STORIED FOUNDATION	SHEET NO:- 8 DWG. NO: 04 Date: 19/01/26	JUBAYER AZAD JIM DRAFTSMAN	Md. Hedayatul Islam ASSISTANT ENGINEER	Atikur Rahman Talukder EXECUTIVE ENGINEER	PROTIVA SARKAR SUPERINTENDING ENGINEER	Md. Tareque Anwar Zahedee CHIEF ENGINEER

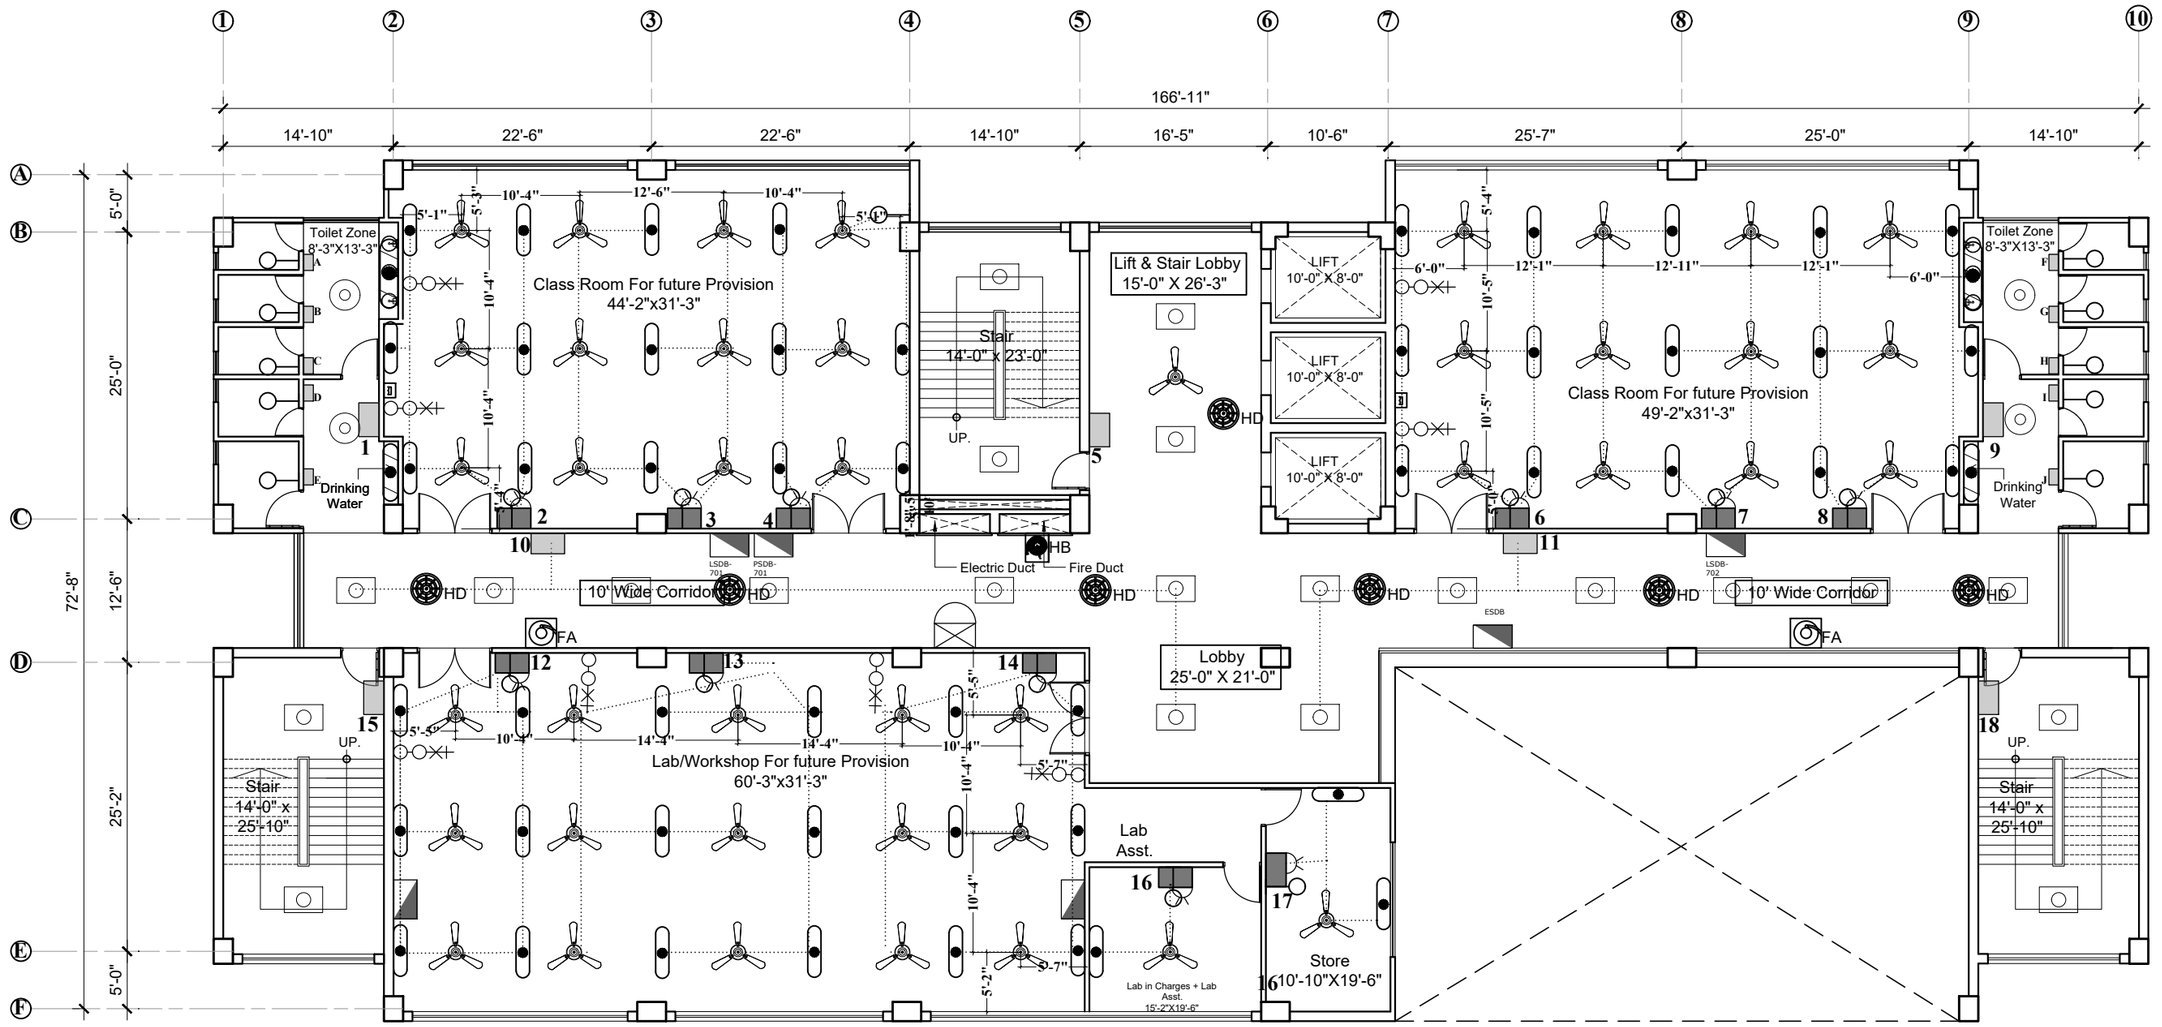

ELECTRICAL FIXTURE LAYOUT PLAN
7TH FLOOR PLAN


EDUCATION ENGINEERING DEPARTMENT MINISTRY OF EDUCATION SHIKKHA BHABAN, DHAKA	NAME OF PROJECT: ESTABLISMENTS OF (04) FOUR NOS ENGINEERING COLLEGE AT CHATTOGRAM,KHULNA,RAJSHAHI & RNGPUR DIVISION	NAME OF WORKS: CONSTRUCTION OF 10(TEN) STORIED ACADEMIC BUILDING (CIVIL ENGINEERING) WITH 10 STORIED FOUNDATION	SHEET NO:- 9 DWG. NO: 04 Date: 19/01/26	JUBAYER AZAD JIM DRAFTSMAN	Md. Hedayatul Islam ASSISTANT ENGINEER	Atikur Rahman Talukder EXECUTIVE ENGINEER	PROTIVA SARKAR SUPERINTENDING ENGINEER	Md. Tareque Anwar Zahedee CHIEF ENGINEER

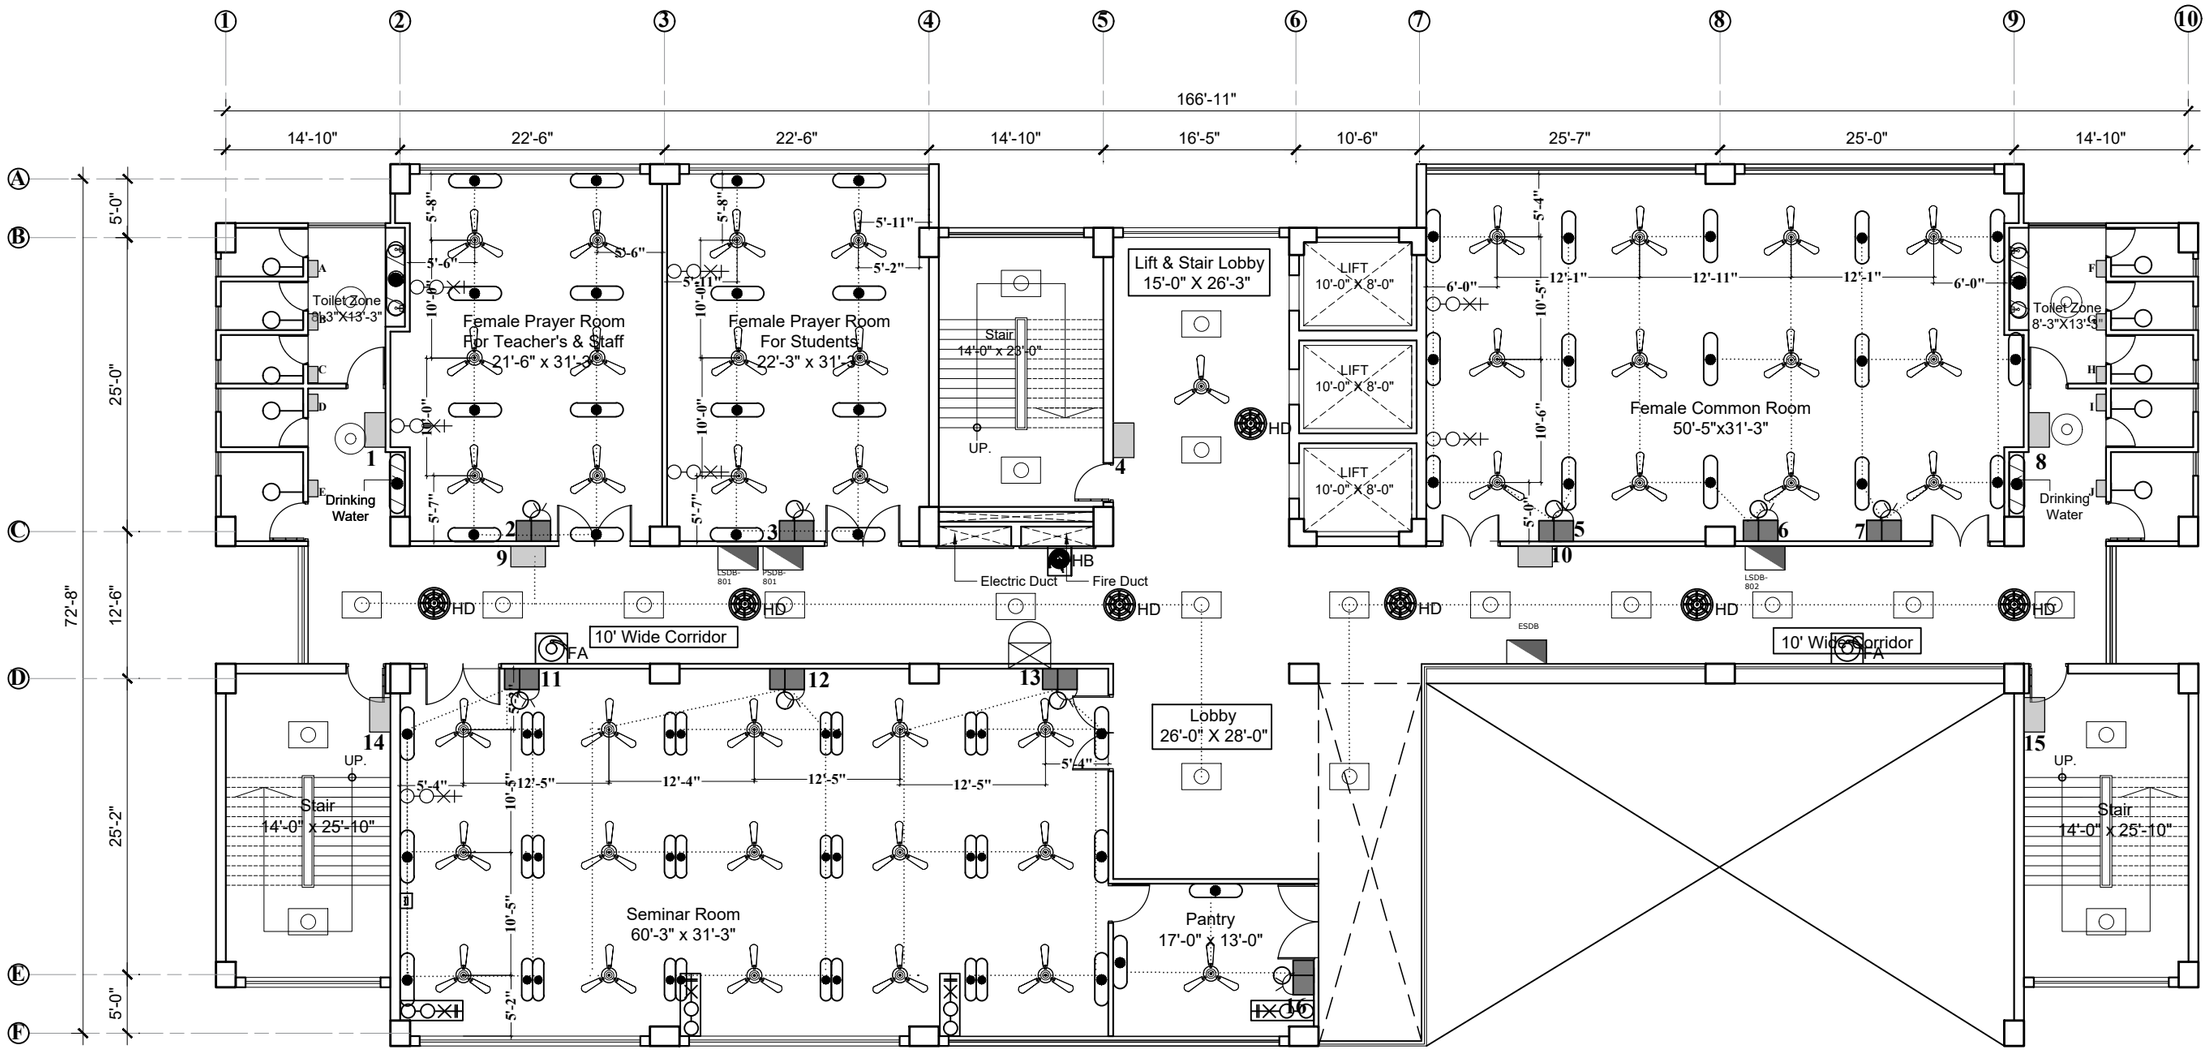

N

ELECTRICAL FIXTURE LAYOUT PLAN
8TH FLOOR PLAN

EDUCATION ENGINEERING DEPARTMENT MINISTRY OF EDUCATION SHIKKHA BHABAN, DHAKA	NAME OF PROJECT: ESTABLISMENTS OF (04) FOUR NOS ENGINEERING COLLEGE AT CHATTOGRAM,KHULNA,RAJSHAHI & RNGPUR DIVISION	NAME OF WORKS: CONSTRUCTION OF 10(TEN) STORIED ACADEMIC BUILDING (CIVIL ENGINEERING) WITH 10 STORIED FOUNDATION	SHEET NO:- 10 DWG. NO: 04 Date: 19/01/26	JUBAYER AZAD JIM DRAFTSMAN	Md. Hedayatul Islam ASSISTANT ENGINEER	Atikur Rahman Talukder EXECUTIVE ENGINEER	PROTIVA SARKAR SUPERINTENDING ENGINEER	Md. Tareque Anwar Zahedee CHIEF ENGINEER

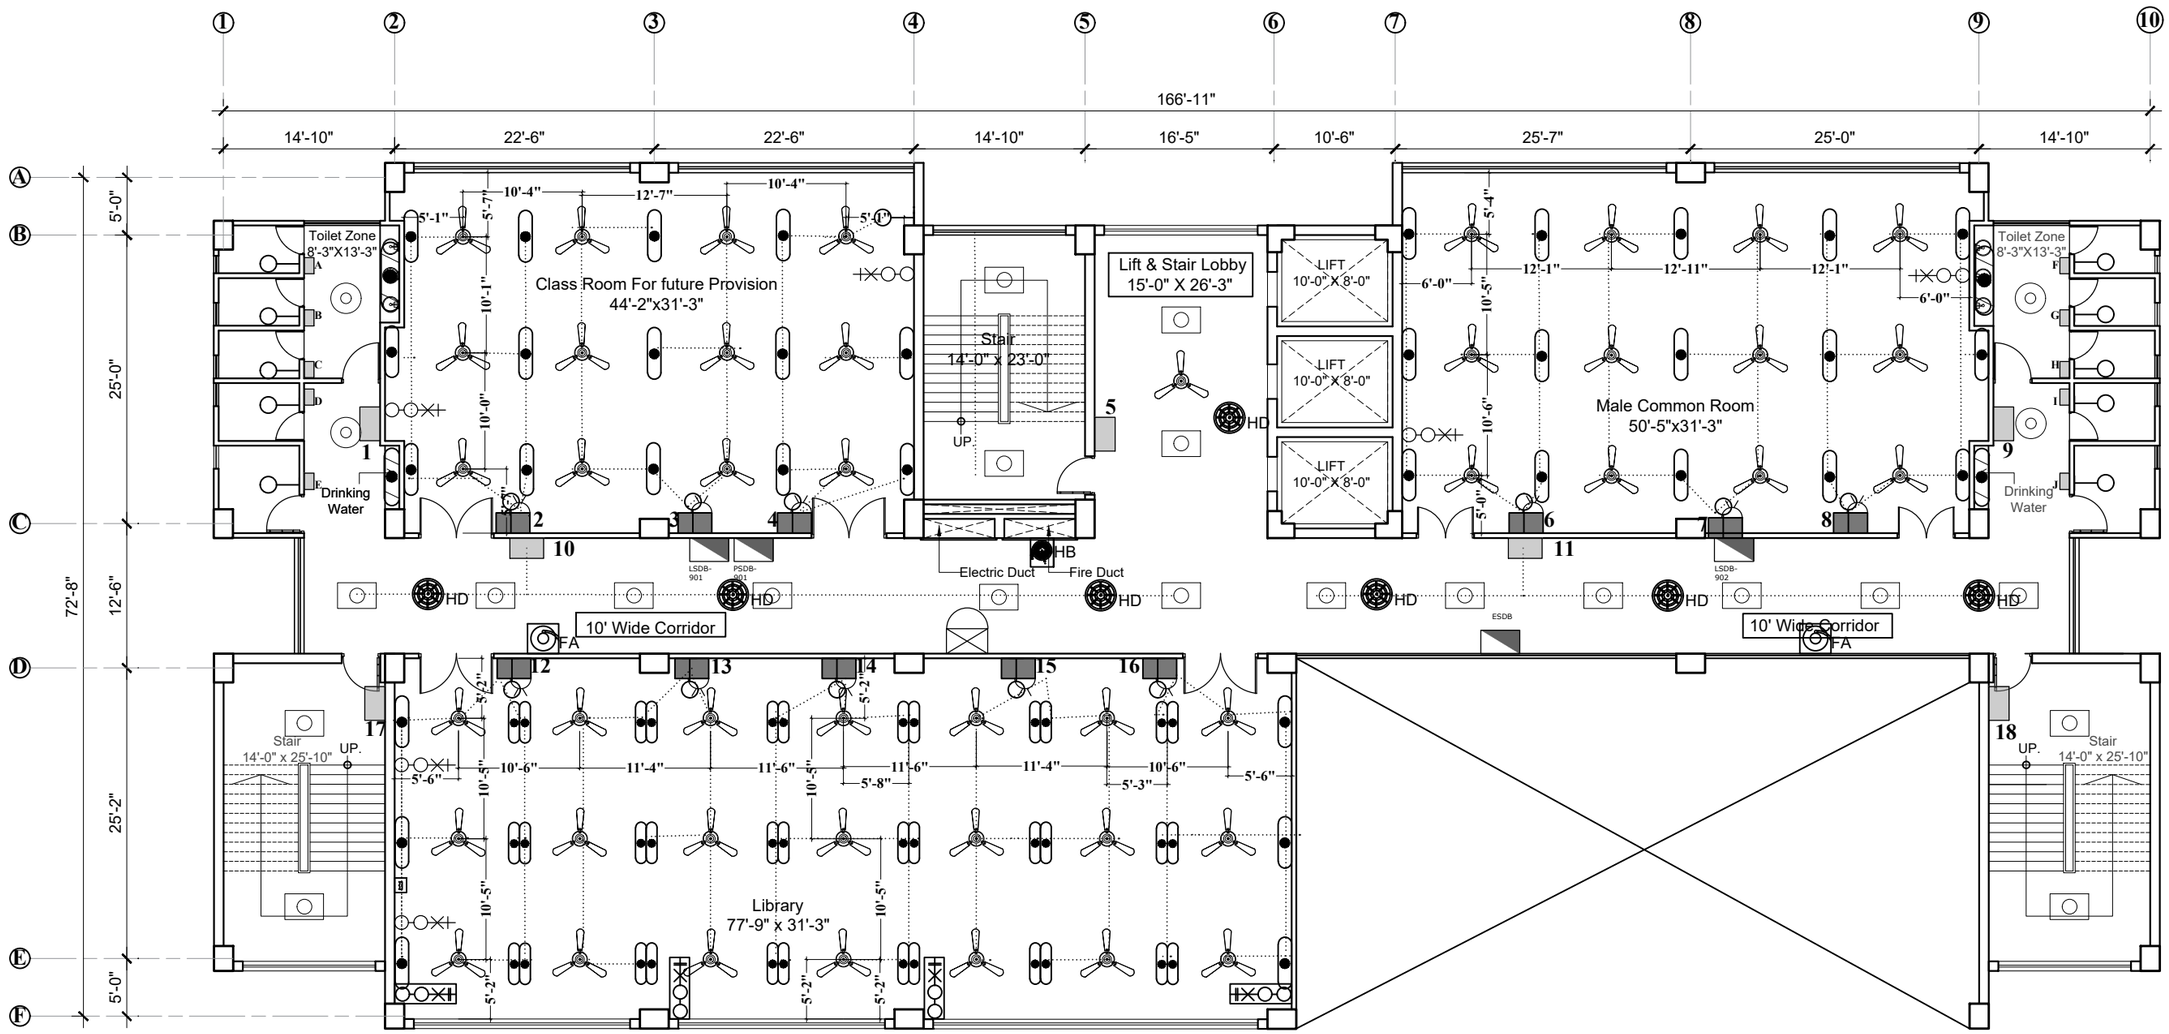


N

ELECTRICAL FIXTURE LAYOUT PLAN
9TH FLOOR PLAN


EDUCATION ENGINEERING DEPARTMENT MINISTRY OF EDUCATION SHIKKHA BHABAN, DHAKA	NAME OF PROJECT: ESTABLISMENTS OF (04) FOUR NOS ENGINEERING COLLEGE AT CHATTOGRAM,KHULNA,RAJSHAHI & RNGPUR DIVISION	NAME OF WORKS: CONSTRUCTION OF 10(TEN) STORIED ACADEMIC BUILDING (CIVIL ENGINEERING) WITH 10 STORIED FOUNDATION	SHEET NO:- 11 DWG. NO: 04 Date: 19/01/26	JUBAYER AZAD JIM DRAFTSMAN	Md. Hedayatul Islam ASSISTANT ENGINEER	Atikur Rahman Talukder EXECUTIVE ENGINEER	PROTIVA SARKAR SUPERINTENDING ENGINEER	Md. Tareque Anwar Zahedee CHIEF ENGINEER

FROM LT TO (PSDB 001)

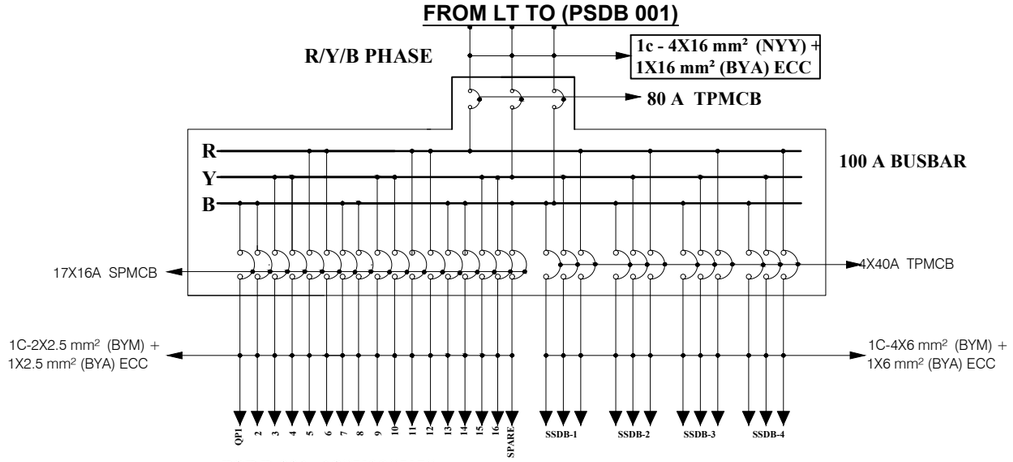

PSDB 001=18"X22"X5"
INCOMING=80 A TPMCB
OUTGOING=17X16A SPMCB
4X40A TPMCB


FROM LT TO (PSDB 002)

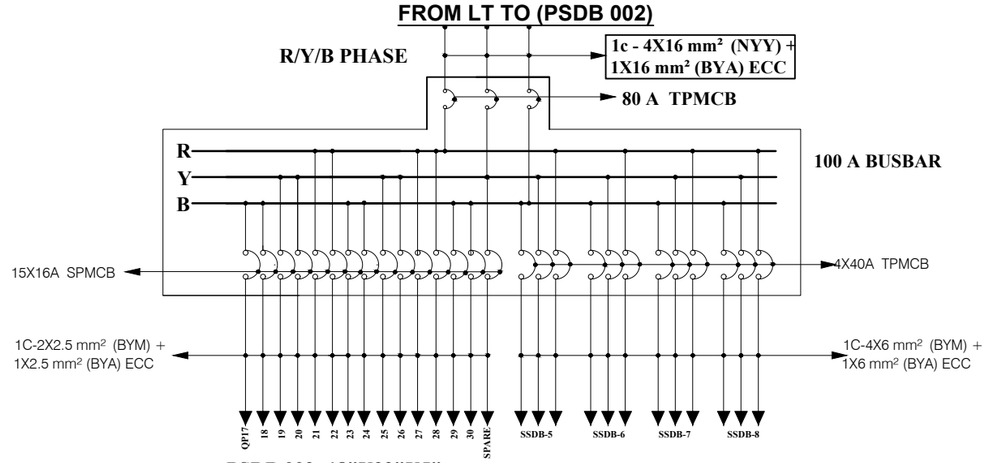

PSDB 002=18"X22"X5"
INCOMING=80 A TPMCB
OUTGOING=15X16A SPMCB
4X40A TPMCB


GF FLOOR

FROM LT TO (LSDB 001)

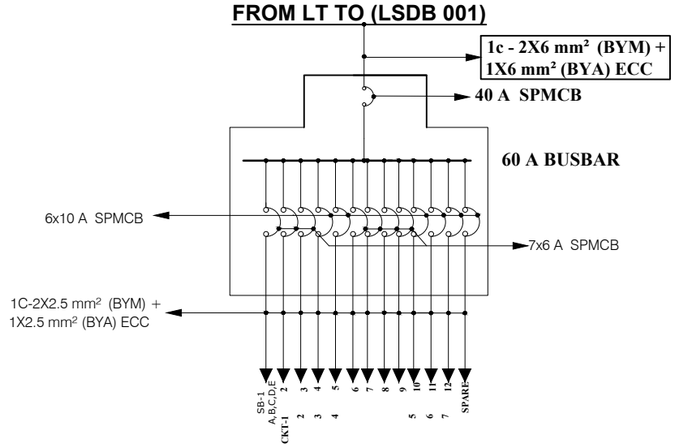

LSDB 001=15"X18"X5"
INCOMING=40 A SPMCB
OUTGOING=6X10A SPMCB
7X6A SPMCB

FROM LT TO (LSDB 002)

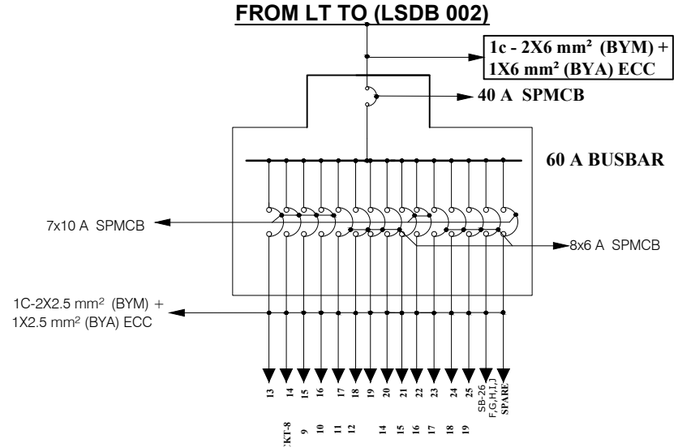


LSDB 002=15"X18"X5"
INCOMING=40 A SPMCB
OUTGOING=8X6A SPMCB
7X6A SPMCB

GF FLOOR


EDUCATION ENGINEERING DEPARTMENT MINISTRY OF EDUCATION SHIKKHA BHABAN, DHAKA	NAME OF PROJECT: ESTABLISMENTS OF (04) FOUR NOS ENGINEERING COLLEGE AT CHATTOGRAM,KHULNA,RAJSHAHI & RNGPUR DIVISION	NAME OF WORKS: CONSTRUCTION OF 10(TEN) STORIED ACADEMIC BUILDING (CIVIL ENGINEERING) WITH 10 STORIED FOUNDATION	SHEET NO:- 12 DWG. NO: 04 Date: 19/01/26	JUBAYER AZAD JIM DRAFTSMAN	Md. Hedayatul Islam ASSISTANT ENGINEER	Atikur Rahman Talukder EXECUTIVE ENGINEER	PROTIVA SARKAR SUPERINTENDING ENGINEER	Md. Tareque Anwar Zahedee CHIEF ENGINEER

FROM LT TO (PSDB 101)

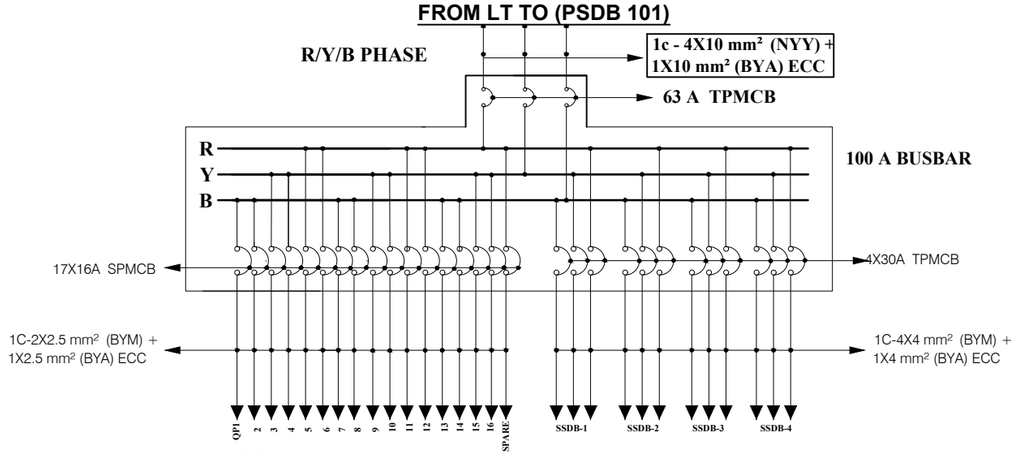

PSDB 101=18"X22"X5"
INCOMING=80 A TPMCB
OUTGOING=17X16A SPMCB
4X40A TPMCB


FROM LT TO (PSDB 102)

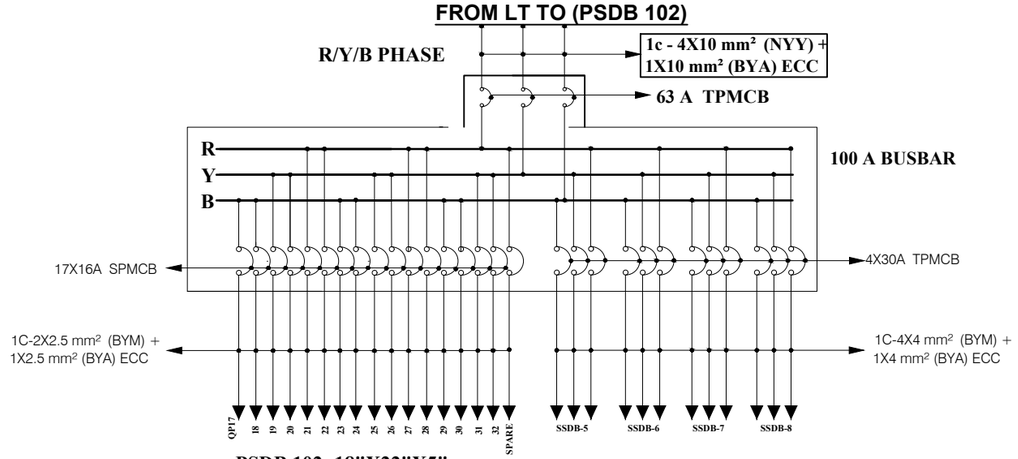

PSDB 102=18"X22"X5"
INCOMING=63 A TPMCB
OUTGOING=17X16A SPMCB
4X40A TPMCB


1st FLOOR

FROM LT TO (LSDB 101)

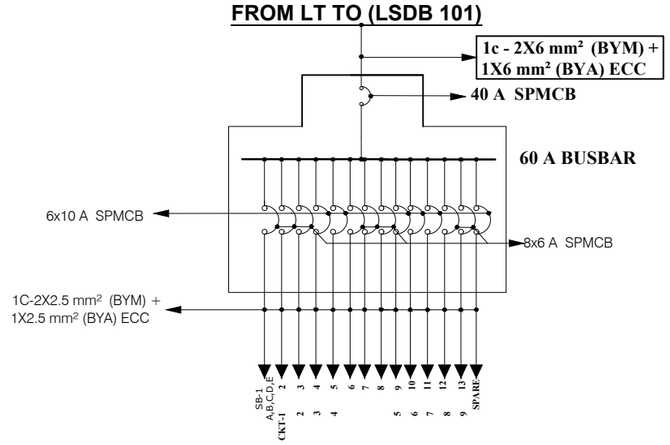

LSDB 101=15"X18"X5"
INCOMING=40 A SPMCB
OUTGOING=6X10A SPMCB
8X6A SPMCB

FROM LT TO (LSDB 102)

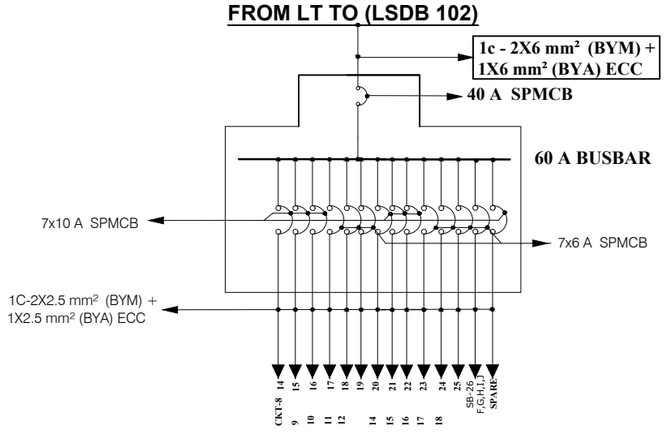


LSDB 102=15"X18"X5"
INCOMING=40 A SPMCB
OUTGOING=7X10A SPMCB
7X6A SPMCB

1st FLOOR


EDUCATION ENGINEERING DEPARTMENT MINISTRY OF EDUCATION SHIKKHA BHABAN, DHAKA	NAME OF PROJECT: ESTABLISMENTS OF (04) FOUR NOS ENGINEERING COLLEGE AT CHATTOGRAM,KHULNA,RAJSHAHI & RNGPUR DIVISION	NAME OF WORKS: CONSTRUCTION OF 10(TEN) STORIED ACADEMIC BUILDING (CIVIL ENGINEERING) WITH 10 STORIED FOUNDATION	SHEET NO:- 13 DWG. NO: 04 Date: 19/01/26	JUBAYER AZAD JIM DRAFTSMAN	Md. Hedayatul Islam ASSISTANT ENGINEER	Atikur Rahman Talukder EXECUTIVE ENGINEER	PROTIVA SARKAR SUPERINTENDING ENGINEER	Md. Tareque Anwar Zahedee CHIEF ENGINEER

FROM LT TO (PSDB 201)

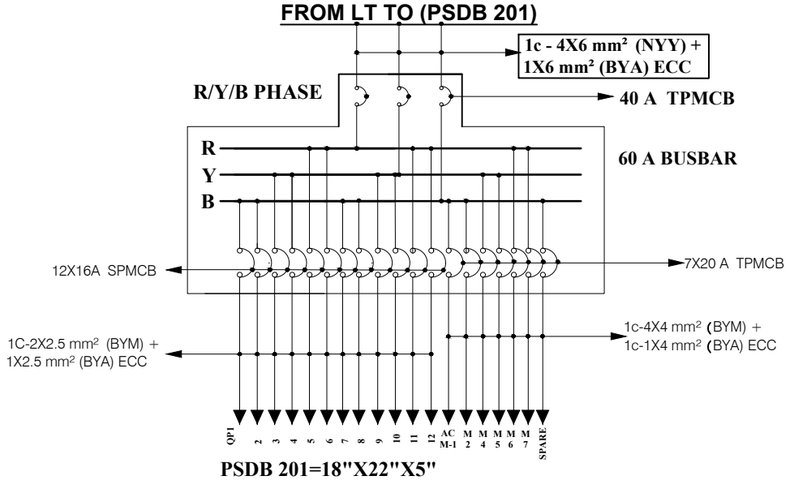

PSDB 201=18"X22"X5"
INCOMING=40 A TPMCB
OUTGOING=12X16A SPMCB
7X20A TPMCB


FROM LT TO (PSDB 202)

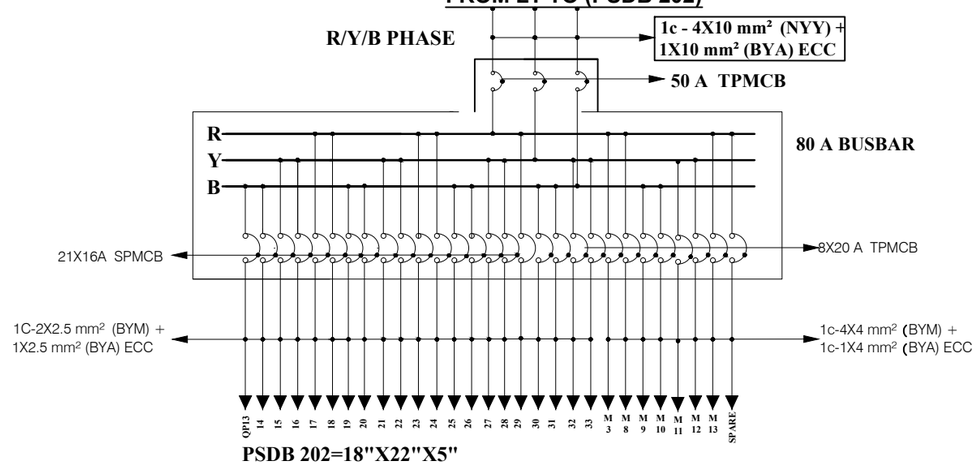

PSDB 202=18"X22"X5"
INCOMING=50 A TPMCB
OUTGOING=21X16A SPMCB
8X20A TPMCB


2ND FLOOR

FROM LT TO (LSDB 201)

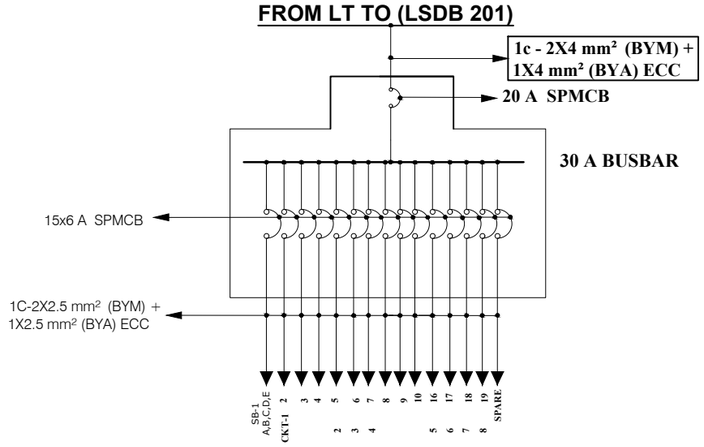

LSDB 201=15"X18"X5"
INCOMING=20 A SPMCB
OUTGOING=15X6A SPMCB

FROM LT TO (LSDB 202)

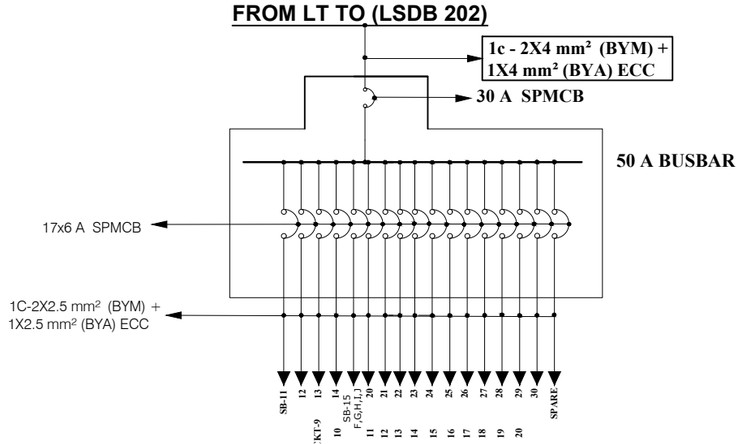


LSDB 202=15"X18"X5"
INCOMING=30 A SPMCB
OUTGOING=17X6A SPMCB

2ND FLOOR

EDUCATION ENGINEERING DEPARTMENT MINISTRY OF EDUCATION SHIKKHA BHABAN, DHAKA	NAME OF PROJECT: ESTABLISMENTS OF (04) FOUR NOS ENGINEERING COLLEGE AT CHATTOGRAM,KHULNA,RAJSHAHI & RNGPUR DIVISION	NAME OF WORKS: CONSTRUCTION OF 10(TEN) STORIED ACADEMIC BUILDING (CIVIL ENGINEERING) WITH 10 STORIED FOUNDATION	SHEET NO:- 14 DWG. NO: 04 Date: 19/01/26	JUBAYER AZAD JIM DRAFTSMAN	Md. Hedayatul Islam ASSISTANT ENGINEER	Atikur Rahman Talukder EXECUTIVE ENGINEER	PROTIVA SARKAR SUPERINTENDING ENGINEER	Md. Tareque Anwar Zahedee CHIEF ENGINEER


FROM LT TO (PSDB 301)

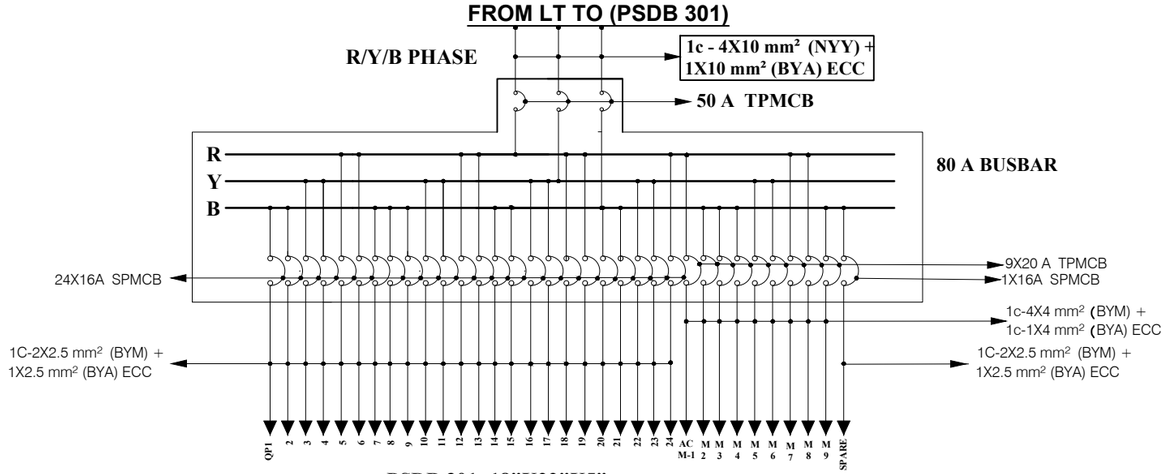

PSDB 301=18"X22"X5"
INCOMING=50 A TPMCB
OUTGOING=25X16A SPMCB
9X20A TPMCB


3RD FLOOR

FROM LT TO (LSDB 301)

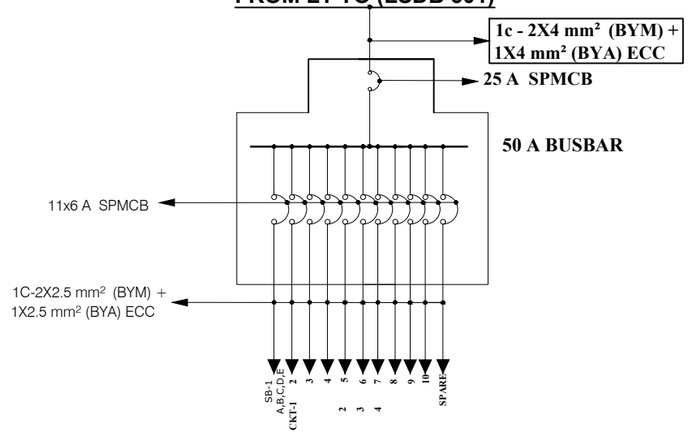

LSDB 301=15"X18"X5"
INCOMING=25 A SPMCB
OUTGOING=11X6A SPMCB

FROM LT TO (LSDB 302)

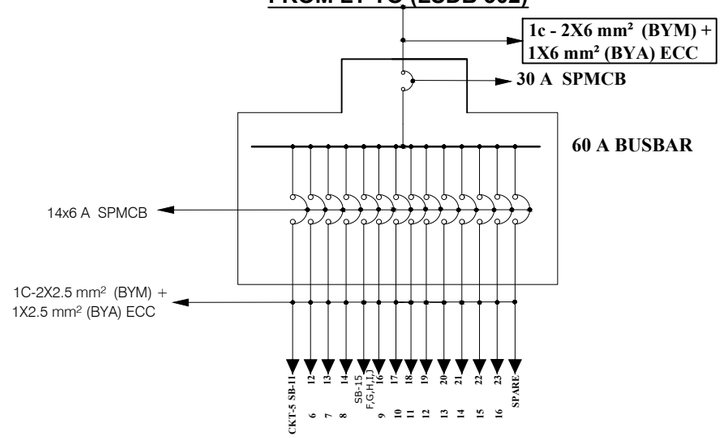


LSDB 302=15"X18"X5"
INCOMING=30 A SPMCB
OUTGOING=14X6A SPMCB

3RD FLOOR

EDUCATION ENGINEERING DEPARTMENT MINISTRY OF EDUCATION SHIKKHA BHABAN, DHAKA	NAME OF PROJECT: ESTABLISMENTS OF (04) FOUR NOS ENGINEERING COLLEGE AT CHATTOGRAM,KHULNA,RAJSHAHI & RNGPUR DIVISION	NAME OF WORKS: CONSTRUCTION OF 10(TEN) STORIED ACADEMIC BUILDING (CIVIL ENGINEERING) WITH 10 STORIED FOUNDATION	SHEET NO:- 15 DWG. NO: 04 Date: 19/01/26	JUBAYER AZAD JIM DRAFTSMAN	Md. Hedayatul Islam ASSISTANT ENGINEER	Atikur Rahman Talukder EXECUTIVE ENGINEER	PROTIVA SARKAR SUPERINTENDING ENGINEER	Md. Tareque Anwar Zahedee CHIEF ENGINEER


FROM LT TO (PSDB 401)

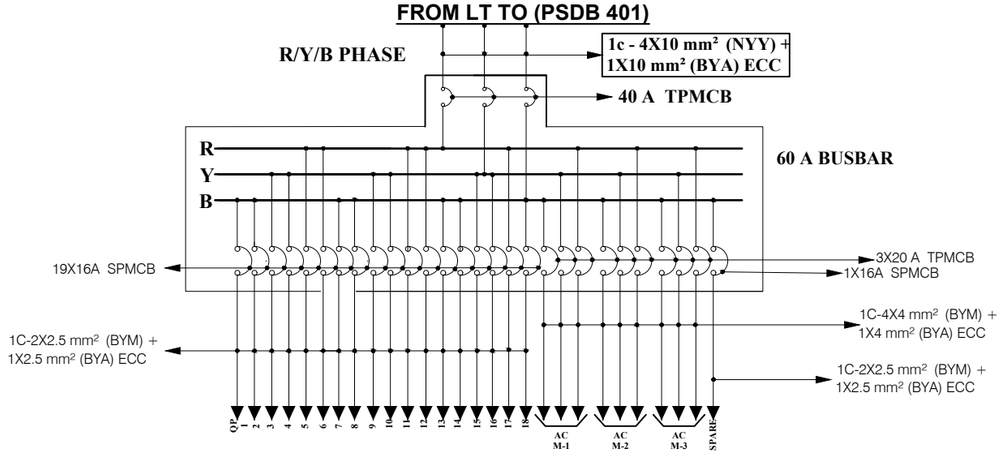

PSDB 401=18"X22"X5"
INCOMING=40 A TPMCB
OUTGOING=20X16A SPMCB
3X20A TPMCB


4TH FLOOR

FROM LT TO (LSDB 401)

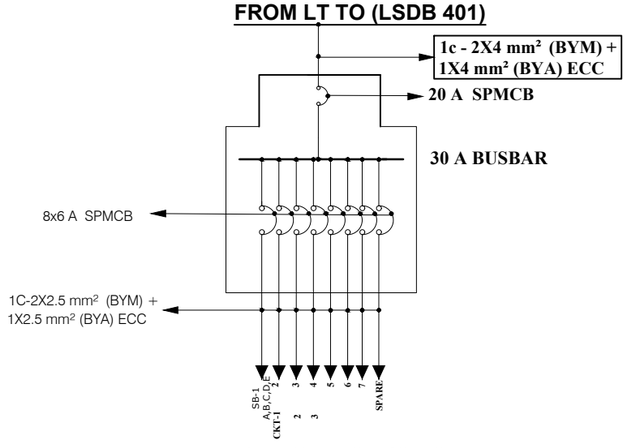

LSDB 401=15"X18"X5"
INCOMING=20 A SPMCB
OUTGOING=8X6A SPMCB

FROM LT TO (LSDB 402)

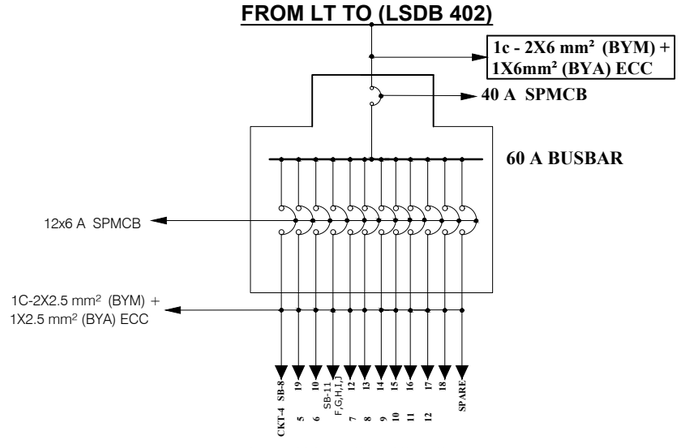


LSDB 402=15"X18"X5"
INCOMING=40 A SPMCB
OUTGOING=12X6A SPMCB

4TH FLOOR


EDUCATION ENGINEERING DEPARTMENT MINISTRY OF EDUCATION SHIKKHA BHABAN, DHAKA	NAME OF PROJECT: ESTABLISMENTS OF (04) FOUR NOS ENGINEERING COLLEGE AT CHATTOGRAM,KHULNA,RAJSHAHI & RNGPUR DIVISION	NAME OF WORKS: CONSTRUCTION OF 10(TEN) STORIED ACADEMIC BUILDING (CIVIL ENGINEERING) WITH 10 STORIED FOUNDATION	SHEET NO:- 16 DWG. NO: 04 Date: 19/01/26	JUBAYER AZAD JIM DRAFTSMAN	Md. Hedayatul Islam ASSISTANT ENGINEER	Atikur Rahman Talukder EXECUTIVE ENGINEER	PROTIVA SARKAR SUPERINTENDING ENGINEER	Md. Tareque Anwar Zahedee CHIEF ENGINEER

FROM LT TO (PSDB 501)

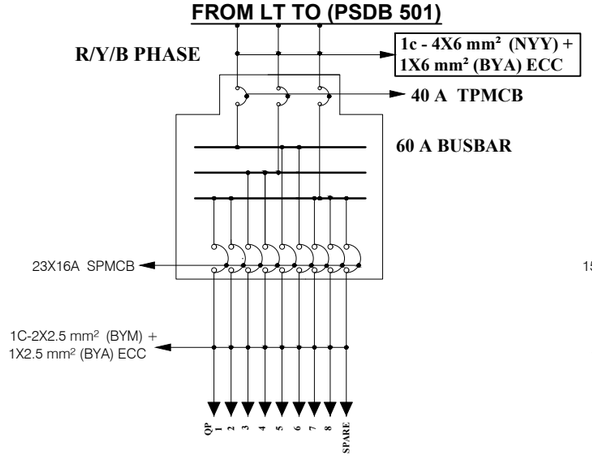

PSDB 501=18"X22"X5"
INCOMING=40 A TPMCB
OUTGOING=9X16A SPMCB


FROM LT TO (PSDB 502)

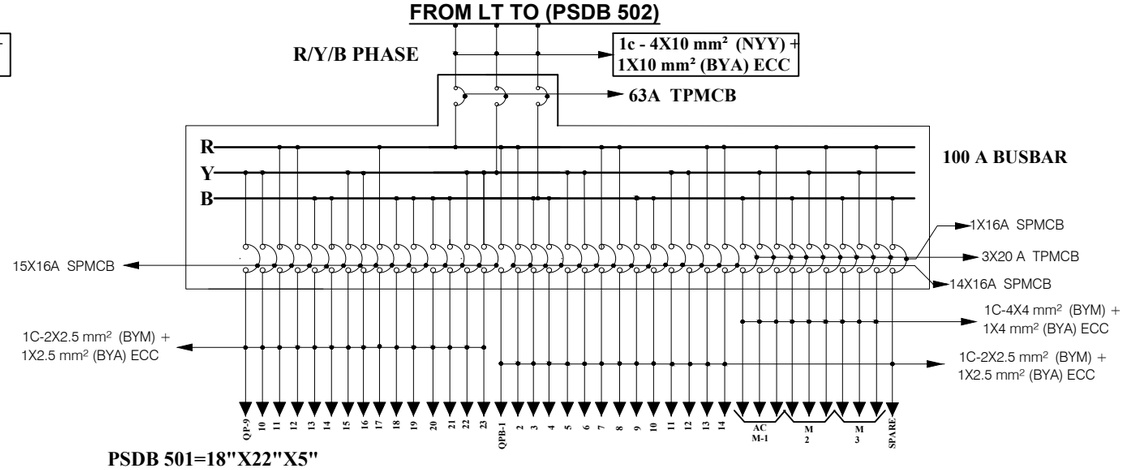

PSDB 501=18"X22"X5"
INCOMING=63 A TPMCB
OUTGOING=16X16A SPMCB
14X16A SPMCB
3X20A TPMCB


5TH FLOOR

FROM LT TO (LSDB 501)

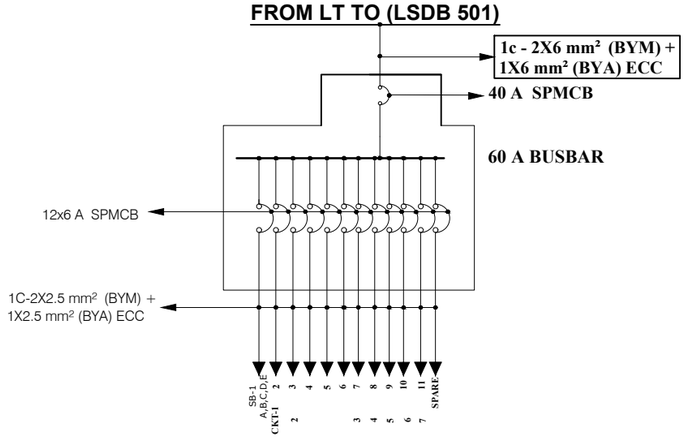

LSDB 501=15"X18"X5"
INCOMING=40 A SPMCB
OUTGOING=12X6A SPMCB

FROM LT TO (LSDB 502)

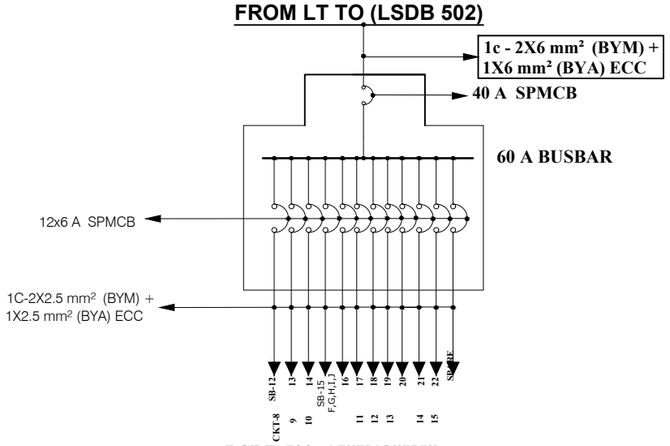


LSDB 502=15"X18"X5"
INCOMING=40 A SPMCB
OUTGOING=12X6A SPMCB

5TH FLOOR

EDUCATION ENGINEERING DEPARTMENT MINISTRY OF EDUCATION SHIKKHA BHABAN, DHAKA	NAME OF PROJECT: ESTABLISMENTS OF (04) FOUR NOS ENGINEERING COLLEGE AT CHATTOGRAM,KHULNA,RAJSHAHI & RNGPUR DIVISION	NAME OF WORKS: CONSTRUCTION OF 10(TEN) STORIED ACADEMIC BUILDING (CIVIL ENGINEERING) WITH 10 STORIED FOUNDATION	SHEET NO:- 17 DWG. NO: 04 Date: 19/01/26	JUBAYER AZAD JIM DRAFTSMAN	Md. Hedayatul Islam ASSISTANT ENGINEER	Atikur Rahman Talukder EXECUTIVE ENGINEER	PROTIVA SARKAR SUPERINTENDING ENGINEER	Md. Tareque Anwar Zahedee CHIEF ENGINEER


FROM LT TO (PSDB 601)

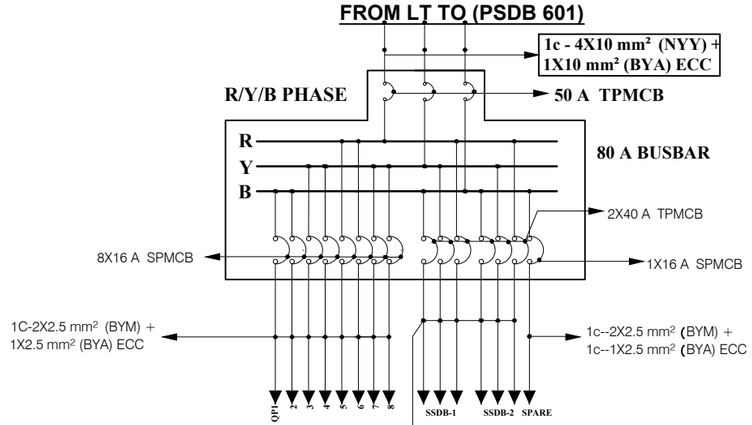

PSDB 601=18"X22"X5"
INCOMING=50 A TPMCB
OUTGOING= 9X16A SPMCB
2X40A TPMCB


6TH FLOOR

FROM LT TO (LSDB 601)

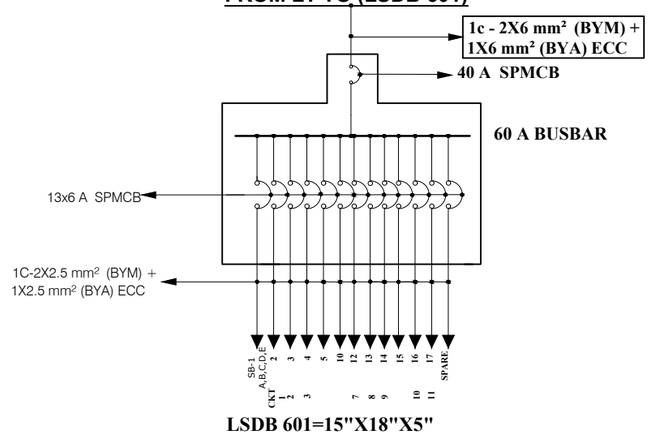

LSDB 601=15"X18"X5"
INCOMING=40 A SPMCB
OUTGOING=13X6A SPMCB

FROM LT TO (LSDB 602)

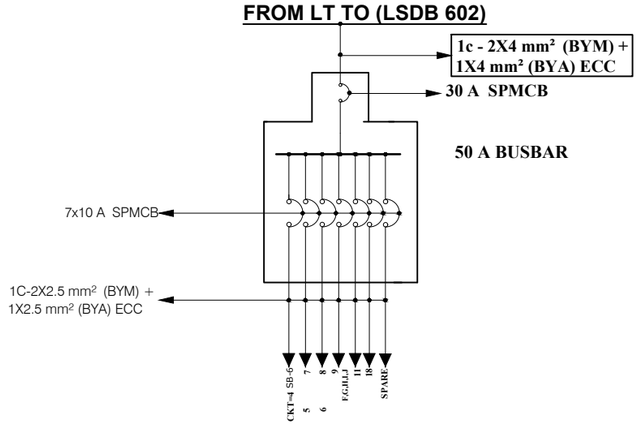


LSDB 602=15"X18"X5"
INCOMING=30 A SPMCB
OUTGOING=7X10A SPMCB

6TH FLOOR

EDUCATION ENGINEERING DEPARTMENT MINISTRY OF EDUCATION SHIKKHA BHABAN, DHAKA	NAME OF PROJECT: ESTABLISMENTS OF (04) FOUR NOS ENGINEERING COLLEGE AT CHATTOGRAM,KHULNA,RAJSHAHI & RNGPUR DIVISION	NAME OF WORKS: CONSTRUCTION OF 10(TEN) STORIED ACADEMIC BUILDING (CIVIL ENGINEERING) WITH 10 STORIED FOUNDATION	SHEET NO:- 18 DWG. NO: 04 Date: 19/01/26	JUBAYER AZAD JIM DRAFTSMAN	Md. Hedayatul Islam ASSISTANT ENGINEER	Atikur Rahman Talukder EXECUTIVE ENGINEER	PROTIVA SARKAR SUPERINTENDING ENGINEER	Md. Tareque Anwar Zahedee CHIEF ENGINEER


FROM LT TO (PSDB 701)

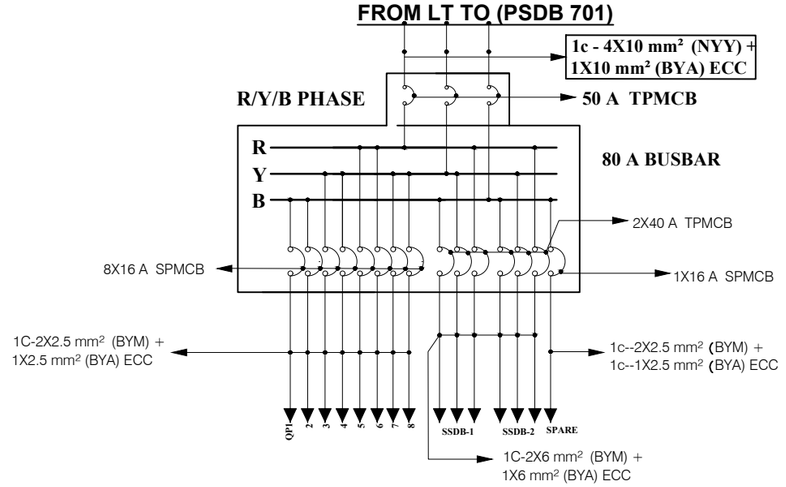

PSDB 701=18"X22"X5"
INCOMING=50 A TPMCB
OUTGOING= 9X16A SPMCB
2X40A TPMCB


7TH FLOOR

FROM LT TO (LSDB 701)

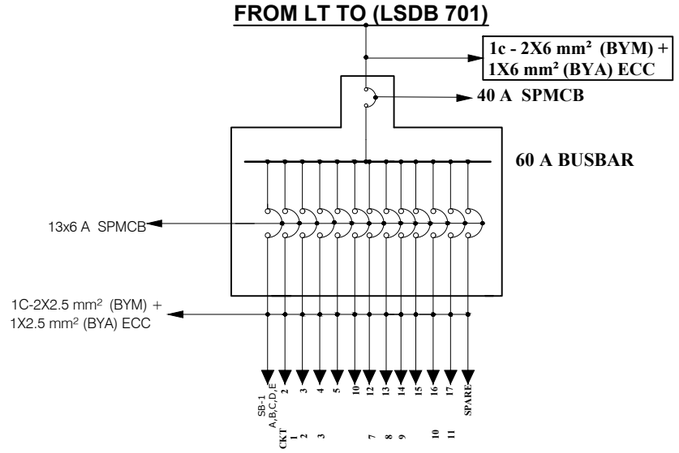

LSDB 301=15"X18"X5"
INCOMING=40 A SPMCB
OUTGOING=13X6A SPMCB

FROM LT TO (LSDB 702)

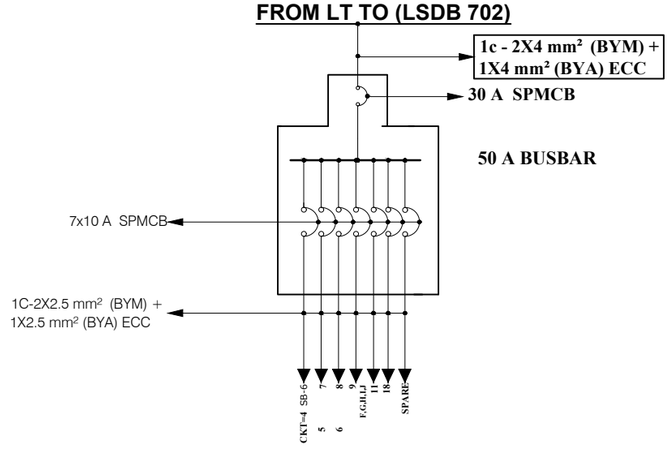


LSDB 302=15"X18"X5"
INCOMING=30 A SPMCB
OUTGOING=7X10A SPMCB

7TH FLOOR

EDUCATION ENGINEERING DEPARTMENT MINISTRY OF EDUCATION SHIKKHA BHABAN, DHAKA	NAME OF PROJECT: ESTABLISMENTS OF (04) FOUR NOS ENGINEERING COLLEGE AT CHATTOGRAM,KHULNA,RAJSHAHI & RNGPUR DIVISION	NAME OF WORKS: CONSTRUCTION OF 10(TEN) STORIED ACADEMIC BUILDING (CIVIL ENGINEERING) WITH 10 STORIED FOUNDATION	SHEET NO:- 19 DWG. NO: 04 Date: 19/01/26	JUBAYER AZAD JIM DRAFTSMAN	Md. Hedayatul Islam ASSISTANT ENGINEER	Atikur Rahman Talukder EXECUTIVE ENGINEER	PROTIVA SARKAR SUPERINTENDING ENGINEER	Md. Tareque Anwar Zahedee CHIEF ENGINEER


FROM LT TO (PSDB 801)

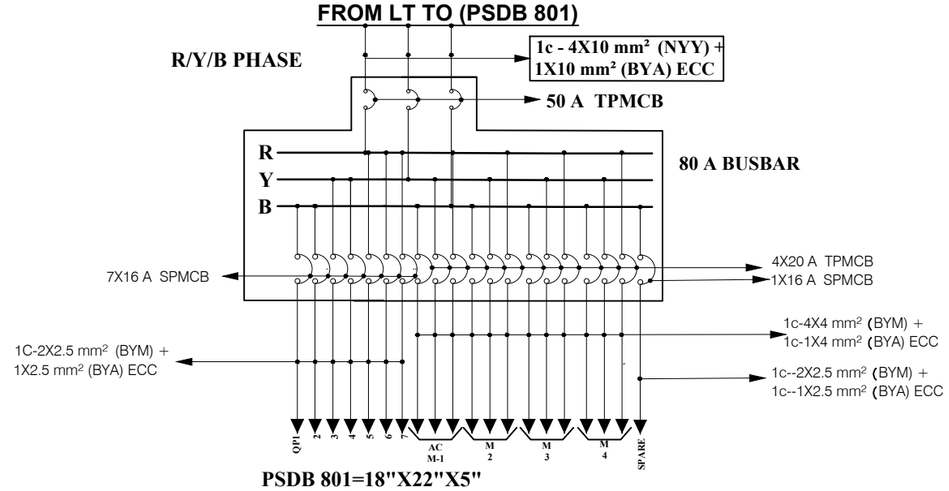

PSDB 801=18"X22"X5"
INCOMING=50 A TPMCB
OUTGOING= 8X16A SPMCB
4X20A TPMCB


8TH FLOOR

FROM LT TO (LSDB 801)

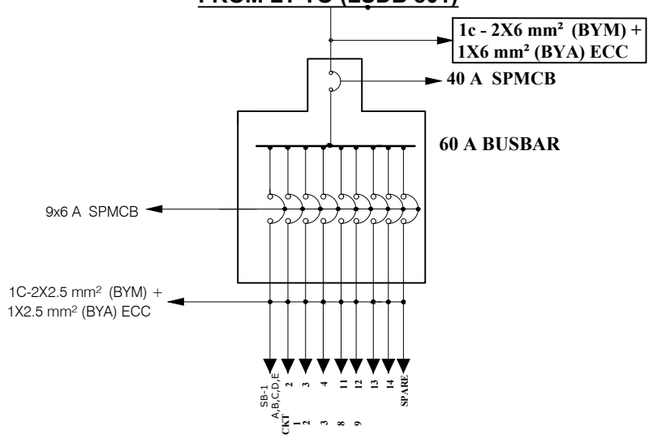

LSDB 801=15"X18"X5"
INCOMING=40 A SPMCB
OUTGOING=8X6A SPMCB


FROM LT TO (LSDB 802)

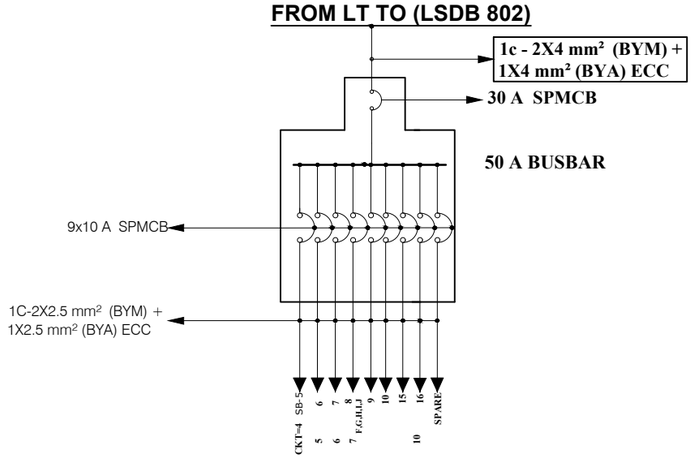

LSDB 802=15"X18"X5"
INCOMING=40 A SPMCB
OUTGOING=9X10A SPMCB


8TH FLOOR

EDUCATION ENGINEERING DEPARTMENT MINISTRY OF EDUCATION SHIKKHA BHABAN, DHAKA	NAME OF PROJECT: ESTABLISMENTS OF (04) FOUR NOS ENGINEERING COLLEGE AT CHATTOGRAM,KHULNA,RAJSHAHI & RNGPUR DIVISION	NAME OF WORKS: CONSTRUCTION OF 10(TEN) STORIED ACADEMIC BUILDING (CIVIL ENGINEERING) WITH 10 STORIED FOUNDATION	SHEET NO:- 20 DWG. NO: 04 Date: 19/01/26	JUBAYER AZAD JIM DRAFTSMAN	Md. Hedayatul Islam ASSISTANT ENGINEER	Atikur Rahman Talukder EXECUTIVE ENGINEER	PROTIVA SARKAR SUPERINTENDING ENGINEER	Md. Tareque Anwar Zahedee CHIEF ENGINEER

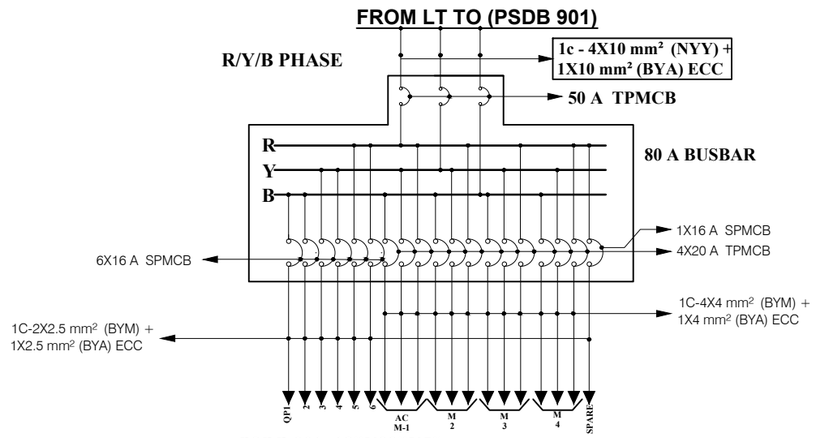


PSDB 901=18"X22"X5"
INCOMING=50 A TPMCB
OUTGOING= 7X16A SPMCB
4X20A TPMCB

9TH FLOOR

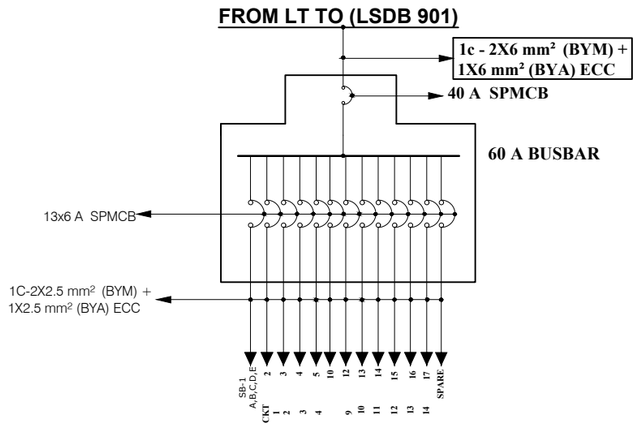


LSDB 901=15"X18"X5"
INCOMING=40 A SPMCB
OUTGOING=13X6A SPMCB

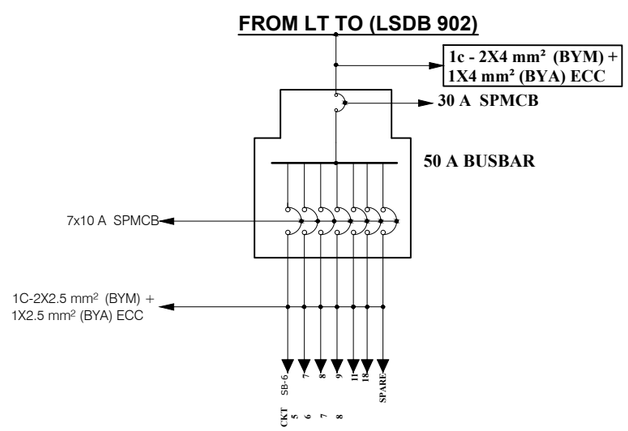

LSDB 902=15"X18"X5"
INCOMING=40 A SPMCB
OUTGOING=7X10A SPMCB

9TH FLOOR


EDUCATION ENGINEERING DEPARTMENT MINISTRY OF EDUCATION SHIKKHA BHABAN, DHAKA	NAME OF PROJECT: ESTABLISMENTS OF (04) FOUR NOS ENGINEERING COLLEGE AT CHATTOGRAM,KHULNA,RAJSHAHI & RNGPUR DIVISION	NAME OF WORKS: CONSTRUCTION OF 10(TEN) STORIED ACADEMIC BUILDING (CIVIL ENGINEERING) WITH 10 STORIED FOUNDATION	SHEET NO:- 21 DWG. NO: 04 Date: 19/01/26	JUBAYER AZAD JIM DRAFTSMAN	Md. Hedayatul Islam ASSISTANT ENGINEER	Atikur Rahman Talukder EXECUTIVE ENGINEER	PROTIVA SARKAR SUPERINTENDING ENGINEER	Md. Tareque Anwar Zahedee CHIEF ENGINEER

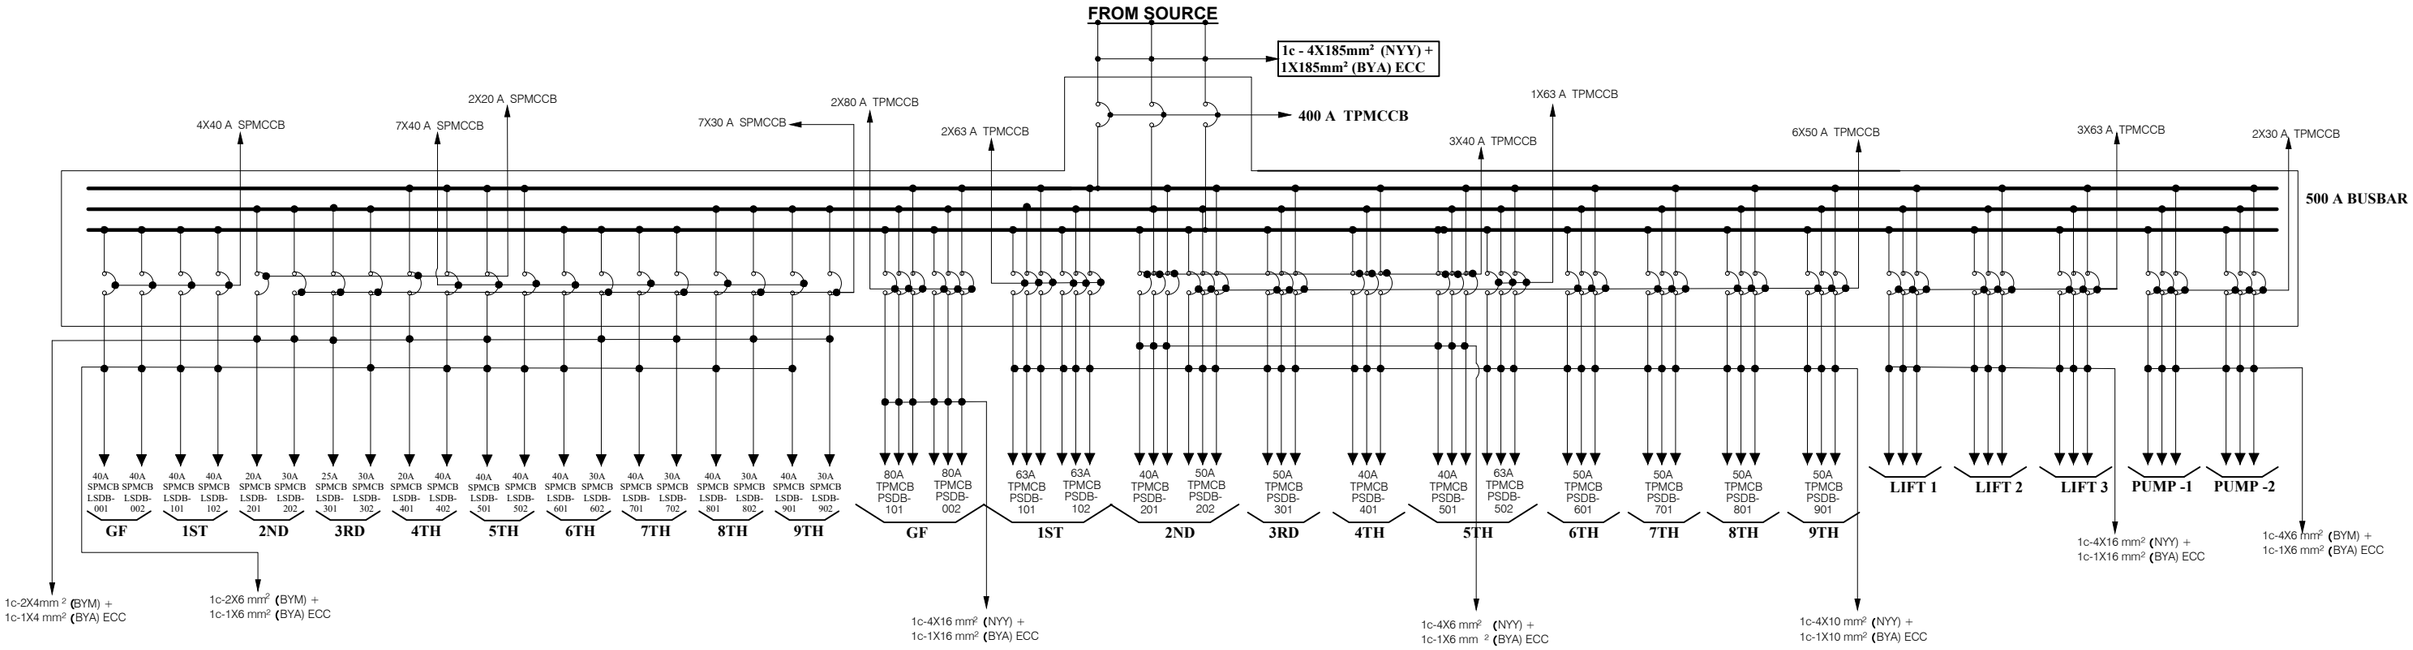


DETAIL DRAWING OF MDB

INCOMING=400A TPMCCB


EDUCATION ENGINEERING DEPARTMENT MINISTRY OF EDUCATION SHIKKHA BHABAN, DHAKA	NAME OF PROJECT: ESTABLISMENTS OF (04) FOUR NOS ENGINEERING COLLEGE AT CHATTOGRAM,KHULNA,RAJSHAHI & RNGPUR DIVISION	NAME OF WORKS: CONSTRUCTION OF 10(TEN) STORIED ACADEMIC BUILDING (CIVIL ENGINEERING) WITH 10 STORIED FOUNDATION	SHEET NO:- 22 DWG. NO: 04 Date: 19/01/26	JUBAYER AZAD JIM DRAFTSMAN	Md. Hedayatul Islam ASSISTANT ENGINEER	Atikur Rahman Talukder EXECUTIVE ENGINEER	PROTIVA SARKAR SUPERINTENDING ENGINEER	Md. Tareque Anwar Zahedee CHIEF ENGINEER

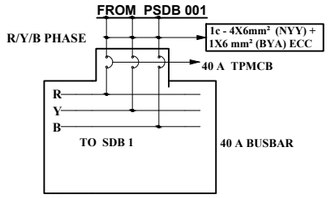


SDB 1
SIZE : 5"X16"X16"
COMPONENTS :
INCOMING = 1X40A TPMCB

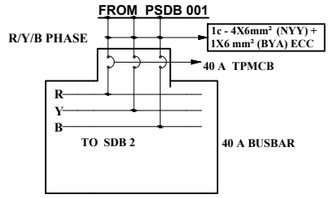


SDB 2
SIZE : 5"X16"X16"
COMPONENTS :
INCOMING = 1X40A TPMCB

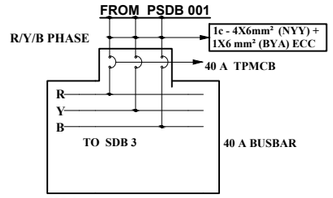


SDB 3
SIZE : 5"X16"X16"
COMPONENTS :
INCOMING = 1X40A TPMCB

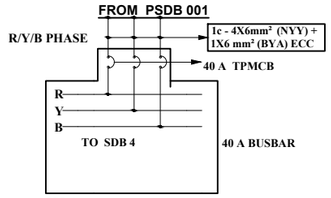


SDB 4
SIZE : 5"X16"X16"
COMPONENTS :
INCOMING = 1X40A TPMCB

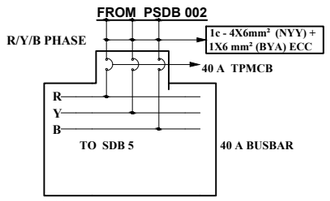


SDB 5
SIZE : 5"X16"X16"
COMPONENTS :
INCOMING = 1X40A TPMCB

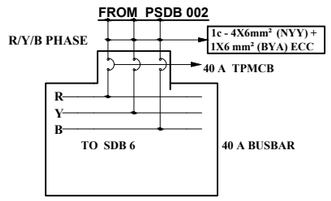

SDB 6
SIZE : 5"X16"X16"
COMPONENTS :
INCOMING = 1X40A TPMCB

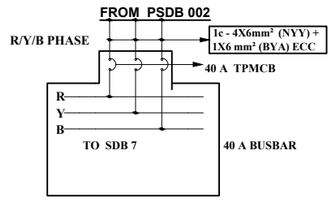


SDB 7
SIZE : 5"X16"X16"
COMPONENTS :
INCOMING = 1X40A TPMCB

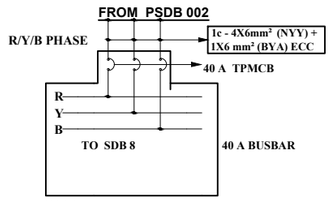


SDB 8
SIZE : 5"X16"X16"
COMPONENTS :
INCOMING = 1X40A TPMCB

GROUND FLOOR

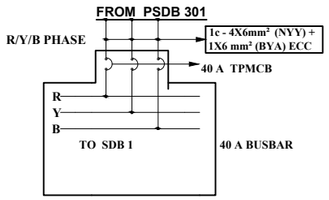


SDB 1
SIZE : 5"X16"X16"
COMPONENTS :
INCOMING = 1X40A TPMCB

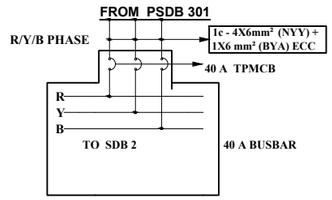


SDB 2
SIZE : 5"X16"X16"
COMPONENTS :
INCOMING = 1X40A TPMCB


6TH FLOOR

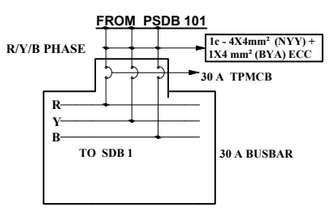


SDB 1
SIZE : 5"X16"X16"
COMPONENTS :
INCOMING = 1X40A TPMCB

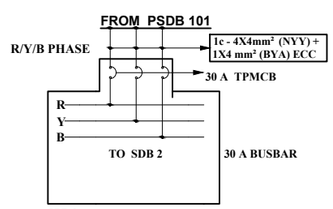


SDB 2
SIZE : 5"X16"X16"
COMPONENTS :
INCOMING = 1X40A TPMCB

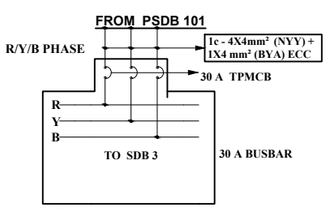


SDB 3
SIZE : 5"X16"X16"
COMPONENTS :
INCOMING = 1X40A TPMCB

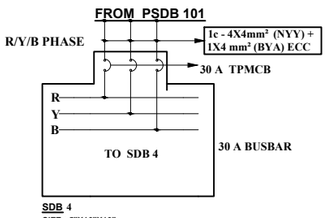


SDB 4
SIZE : 5"X16"X16"
COMPONENTS :
INCOMING = 1X40A TPMCB

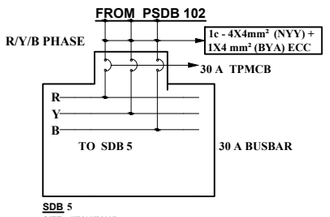


SDB 5
SIZE : 5"X16"X16"
COMPONENTS :
INCOMING = 1X40A TPMCB

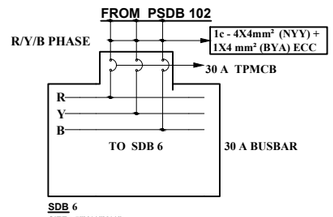

SDB 6
SIZE : 5"X16"X16"
COMPONENTS :
INCOMING = 1X40A TPMCB

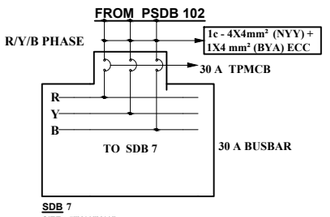


SDB 7
SIZE : 5"X16"X16"
COMPONENTS :
INCOMING = 1X40A TPMCB

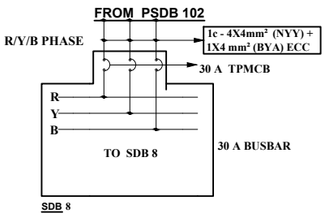


SDB 8
SIZE : 5"X16"X16"
COMPONENTS :
INCOMING = 1X40A TPMCB

1ST FLOOR

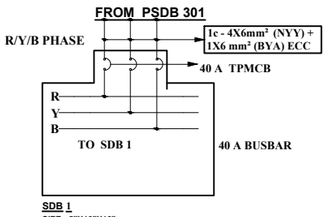


SDB 1
SIZE : 5"X16"X16"
COMPONENTS :
INCOMING = 1X40A TPMCB

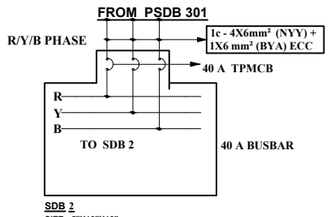

SDB 2
SIZE : 5"X16"X16"
COMPONENTS :
INCOMING = 1X40A TPMCB


7TH FLOOR

EDUCATION ENGINEERING DEPARTMENT MINISTRY OF EDUCATION SHIKKHA BHABAN, DHAKA	NAME OF PROJECT: ESTABLISMENTS OF (04) FOUR NOS ENGINEERING COLLEGE AT CHATTOGRAM,KHULNA,RAJSHAHI & RNGPUR DIVISION	NAME OF WORKS: CONSTRUCTION OF 10(TEN) STORIED ACADEMIC BUILDING (CIVIL ENGINEERING) WITH 10 STORIED FOUNDATION	SHEET NO:- 23 DWG. NO: 04 Date: 19/01/26	JUBAYER AZAD JIM DRAFTSMAN	Md. Hedayatul Islam ASSISTANT ENGINEER	Atikur Rahman Talukder EXECUTIVE ENGINEER	PROTIVA SARKAR SUPERINTENDING ENGINEER	Md. Tareque Anwar Zahedee CHIEF ENGINEER

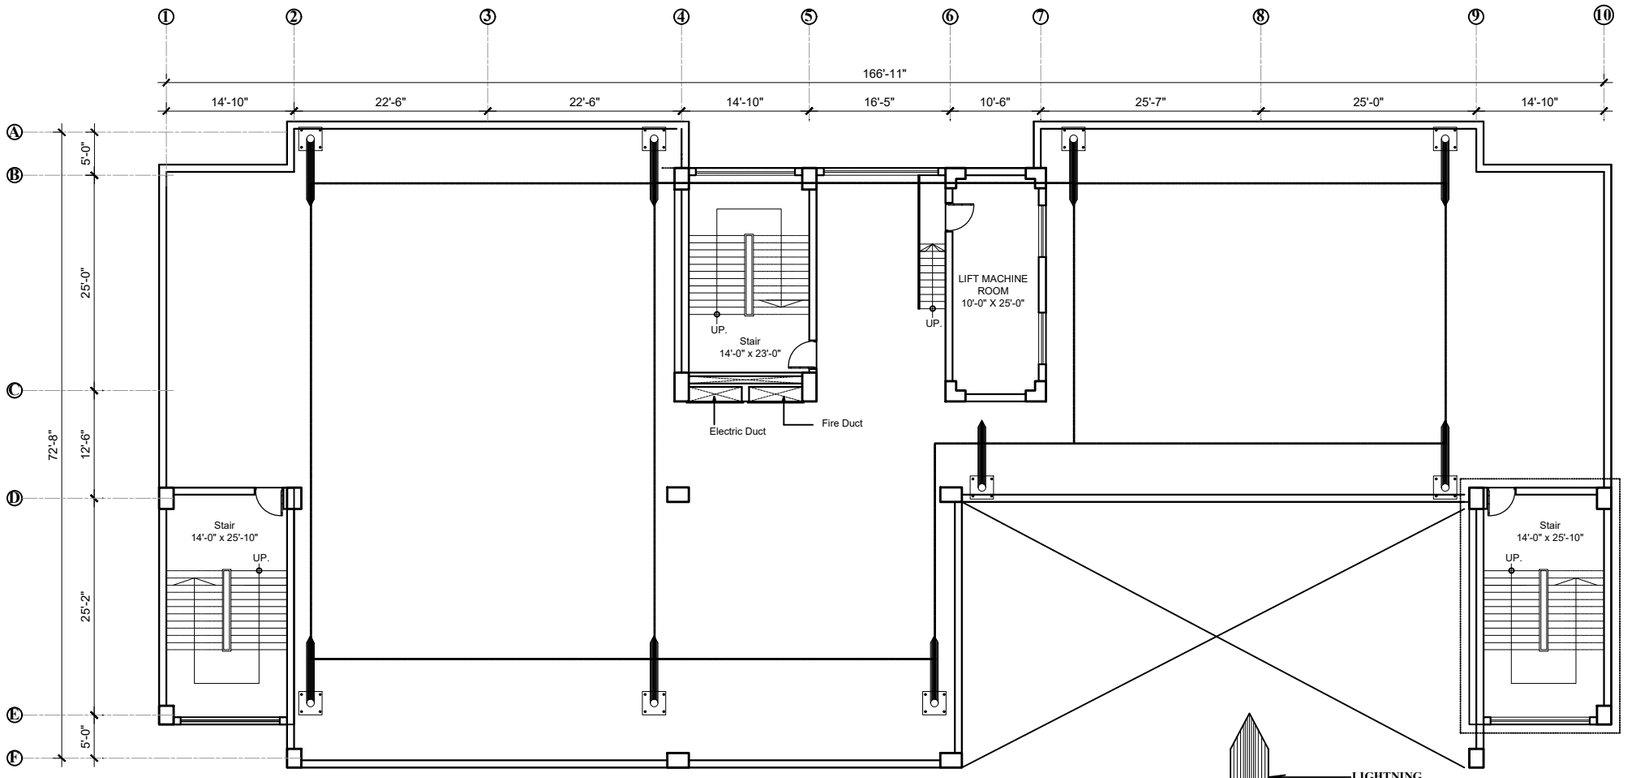


N

ROOF PLAN
AREA=1600 Sft.
Scale= Not to Sacle

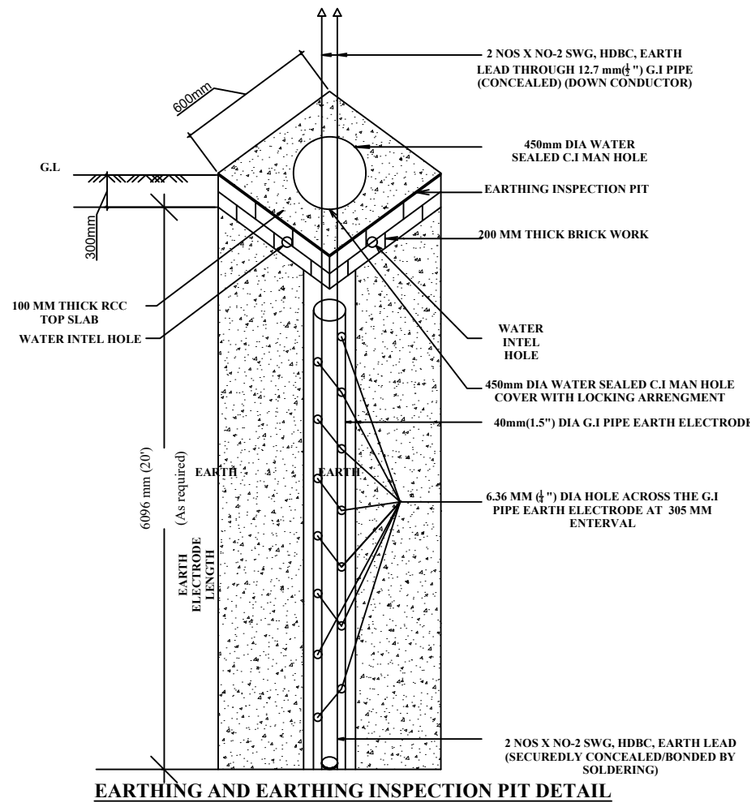

EARTHING AND EARTHING INSPECTION PIT DETAIL

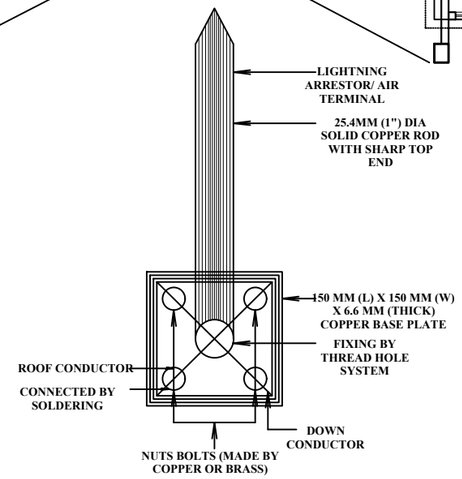

LIGHTNING ARRESTOR/ AIR TERMINAL DETAIL

EDUCATION ENGINEERING DEPARTMENT MINISTRY OF EDUCATION SHIKKHA BHABAN, DHAKA	NAME OF PROJECT: ESTABLISMENTS OF (04) FOUR NOS ENGINEERING COLLEGE AT CHATTOGRAM,KHULNA,RAJSHAHI & RNGPUR DIVISION	NAME OF WORKS: CONSTRUCTION OF 10(TEN) STORIED ACADEMIC BUILDING (CIVIL ENGINEERING) WITH 10 STORIED FOUNDATION	SHEET NO:- 24 DWG. NO: 04 Date: 19/01/26	JUBAYER AZAD JIM DRAFTSMAN	Md. Hedayatul Islam ASSISTANT ENGINEER	Atikur Rahman Talukder EXECUTIVE ENGINEER	PROTIVA SARKAR SUPERINTENDING ENGINEER	Md. Tareque Anwar Zahedee CHIEF ENGINEER